


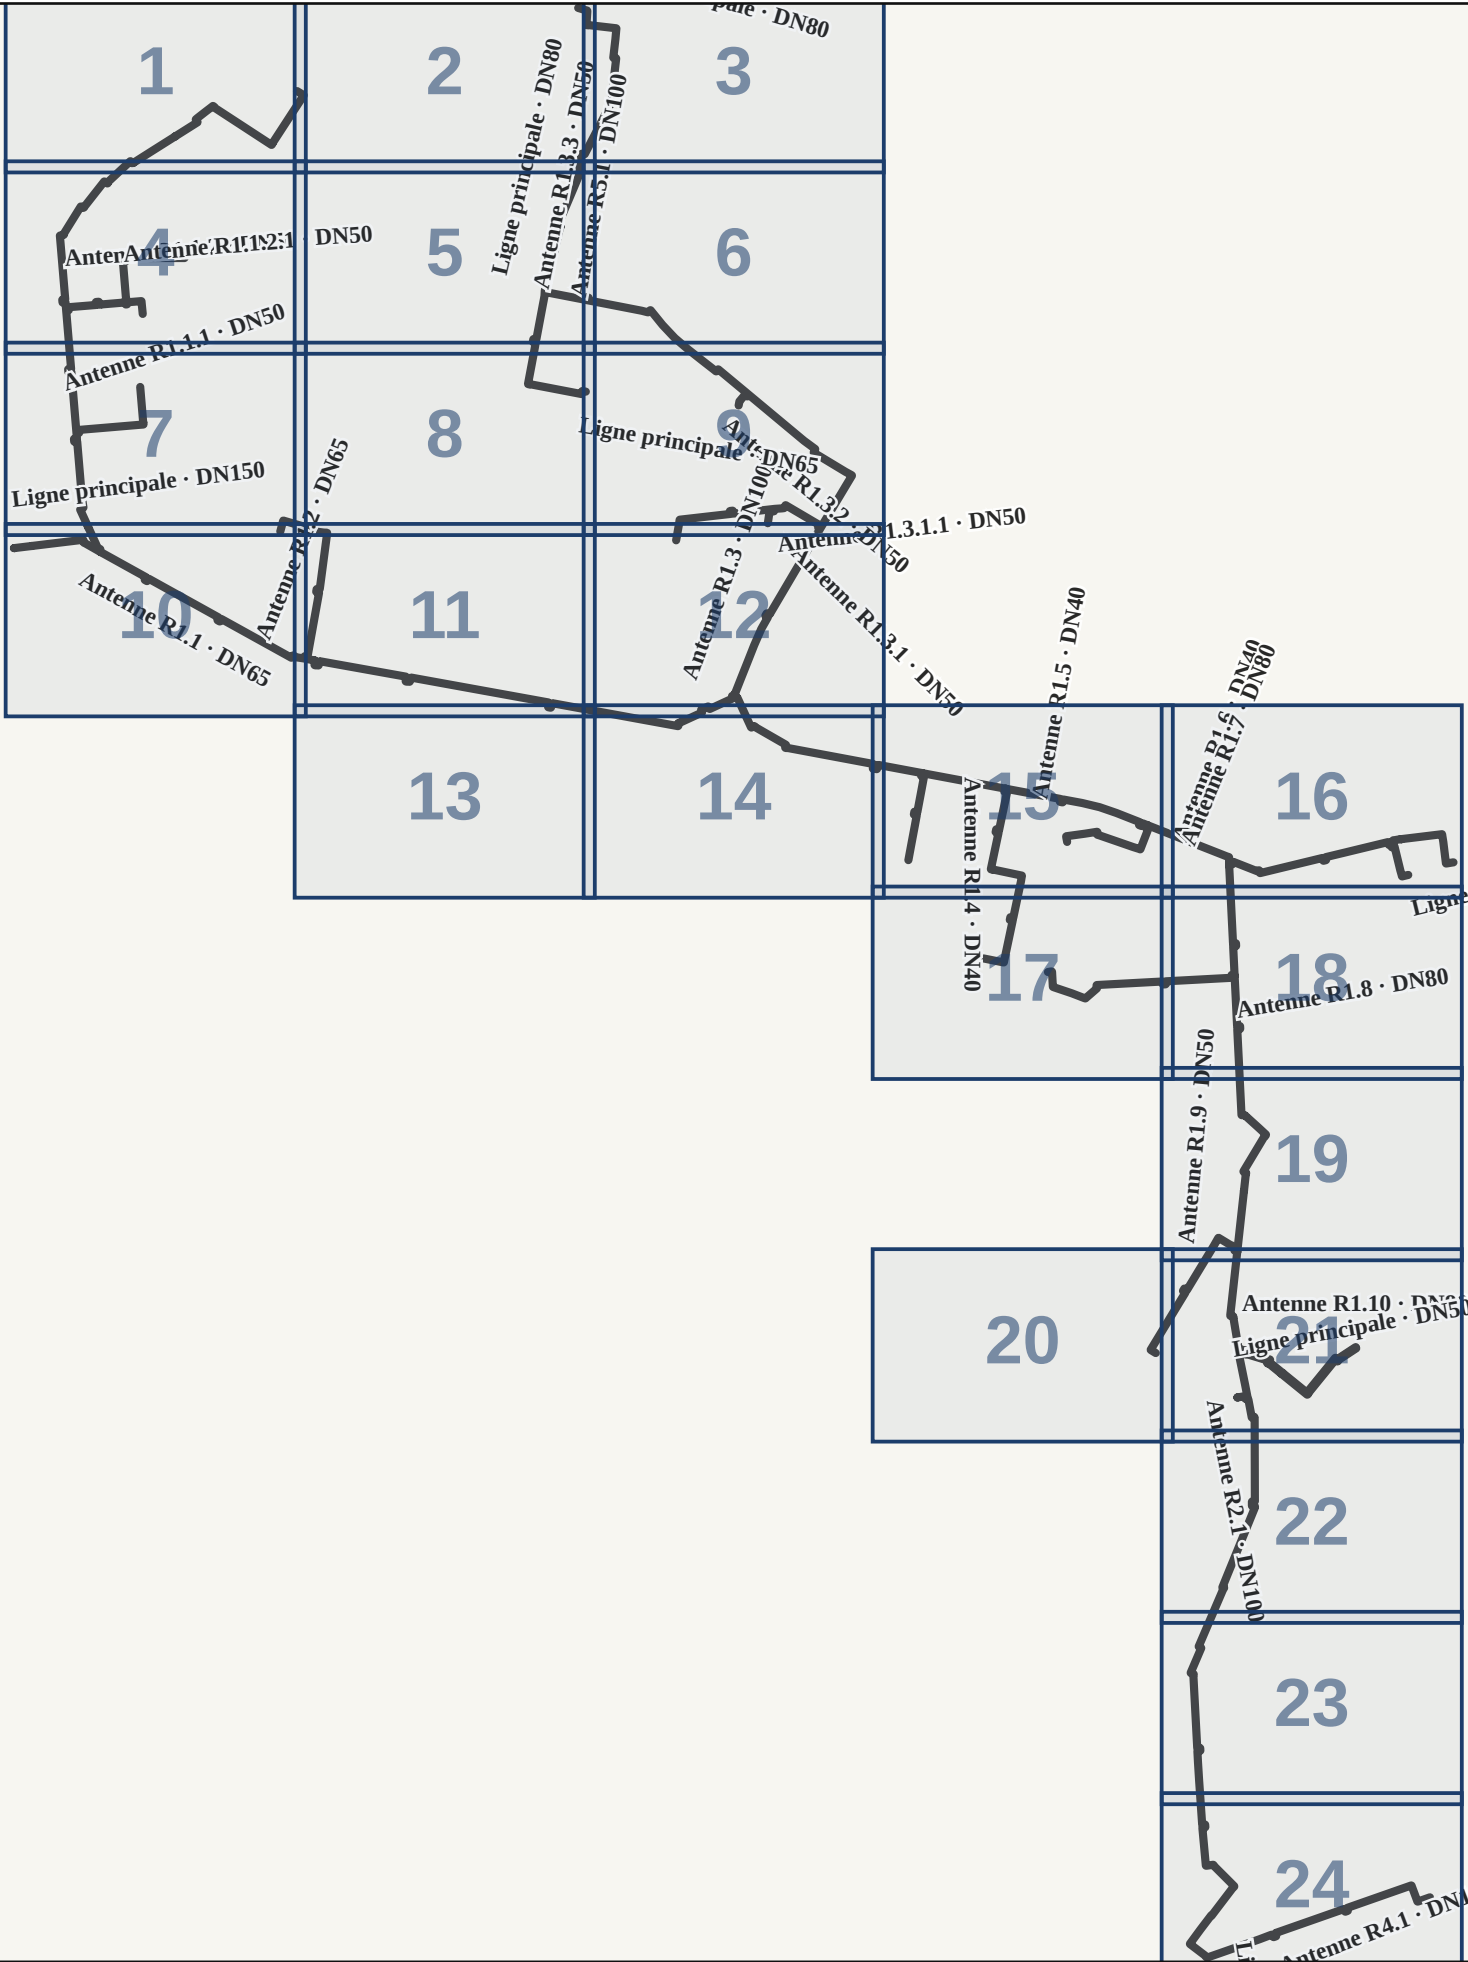


Bain-de-Bretagne — LOGSTOR (DWG calepinage)

Plan des soudures numérotées — plan de découpage (24 planches A3 à l'échelle 1/500)



Bain-de-Bretagne — LOGSTOR (DWG calepinage)
● À souder ● Soudée ● Contrôlée ● Manchonnée ● À reprendre
— aller — retour — vanne — réduction — té



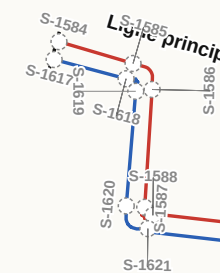

◀ planche 1

► planche 3

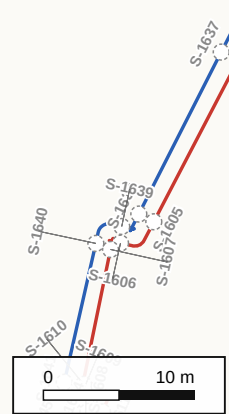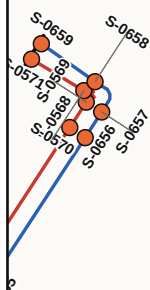

▼ planche 5

Bain-de-Bretagne — LOGSTOR (DWG calepinage)

Plan des soudures numérotées — **planche 2 / 24** · échelle 1/500 sur A3


Bain-de-Bretagne — LOGSTOR (DWG calepinage) · report du carnet de soudage et manchonnage · n° = n° de soudure (pastille = avancement)

● À souder
 ● Soudée
 ● Contrôlée
 ● Manchonnée
 ● À reprendre
 — aller
 — retour
 ⌘ vanne
 ▷ réduction
 ■ té

Planche 2 / 24

édité le 07/10/2026 par Ethan L.

TRACÉ / RCU-COMPAGNON

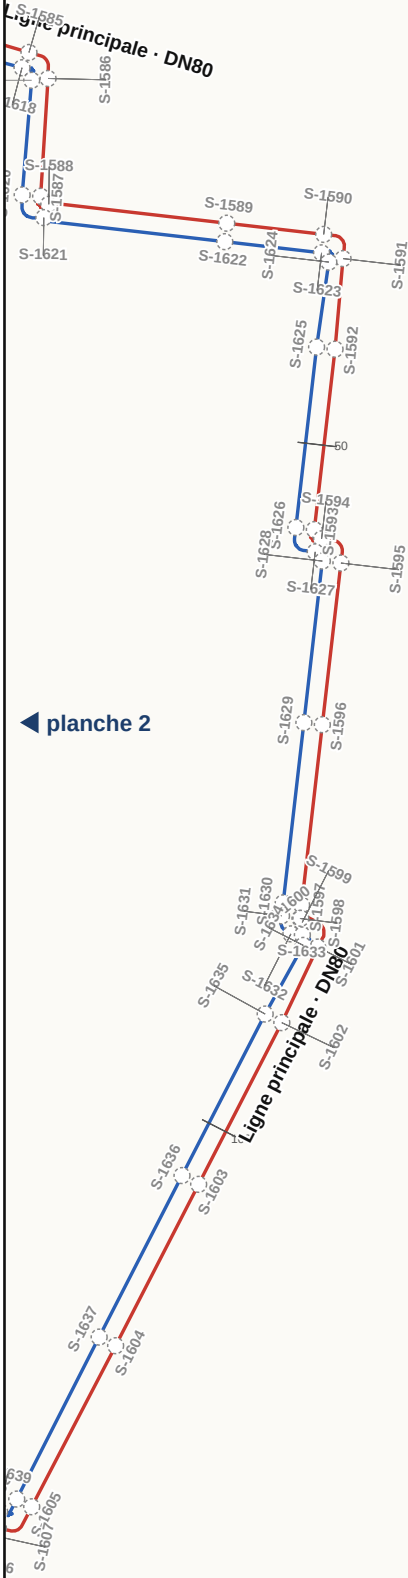

◀ planche 2


▼ planche 6

Bain-de-Bretagne — LOGSTOR (DWG calepinage)

Plan des soudures numérotées — planche 3 / 24 · échelle 1/500 sur A3

Bain-de-Bretagne — LOGSTOR (DWG calepinage) · report du carnet de soudage et manchonnage · n° = n° de soudure (pastille = avancement)


● À souder ● Soudée ● Contrôlée ● Manchonnée ● À reprendre — aller — retour ◀ vanne ▷ réduction ■ té

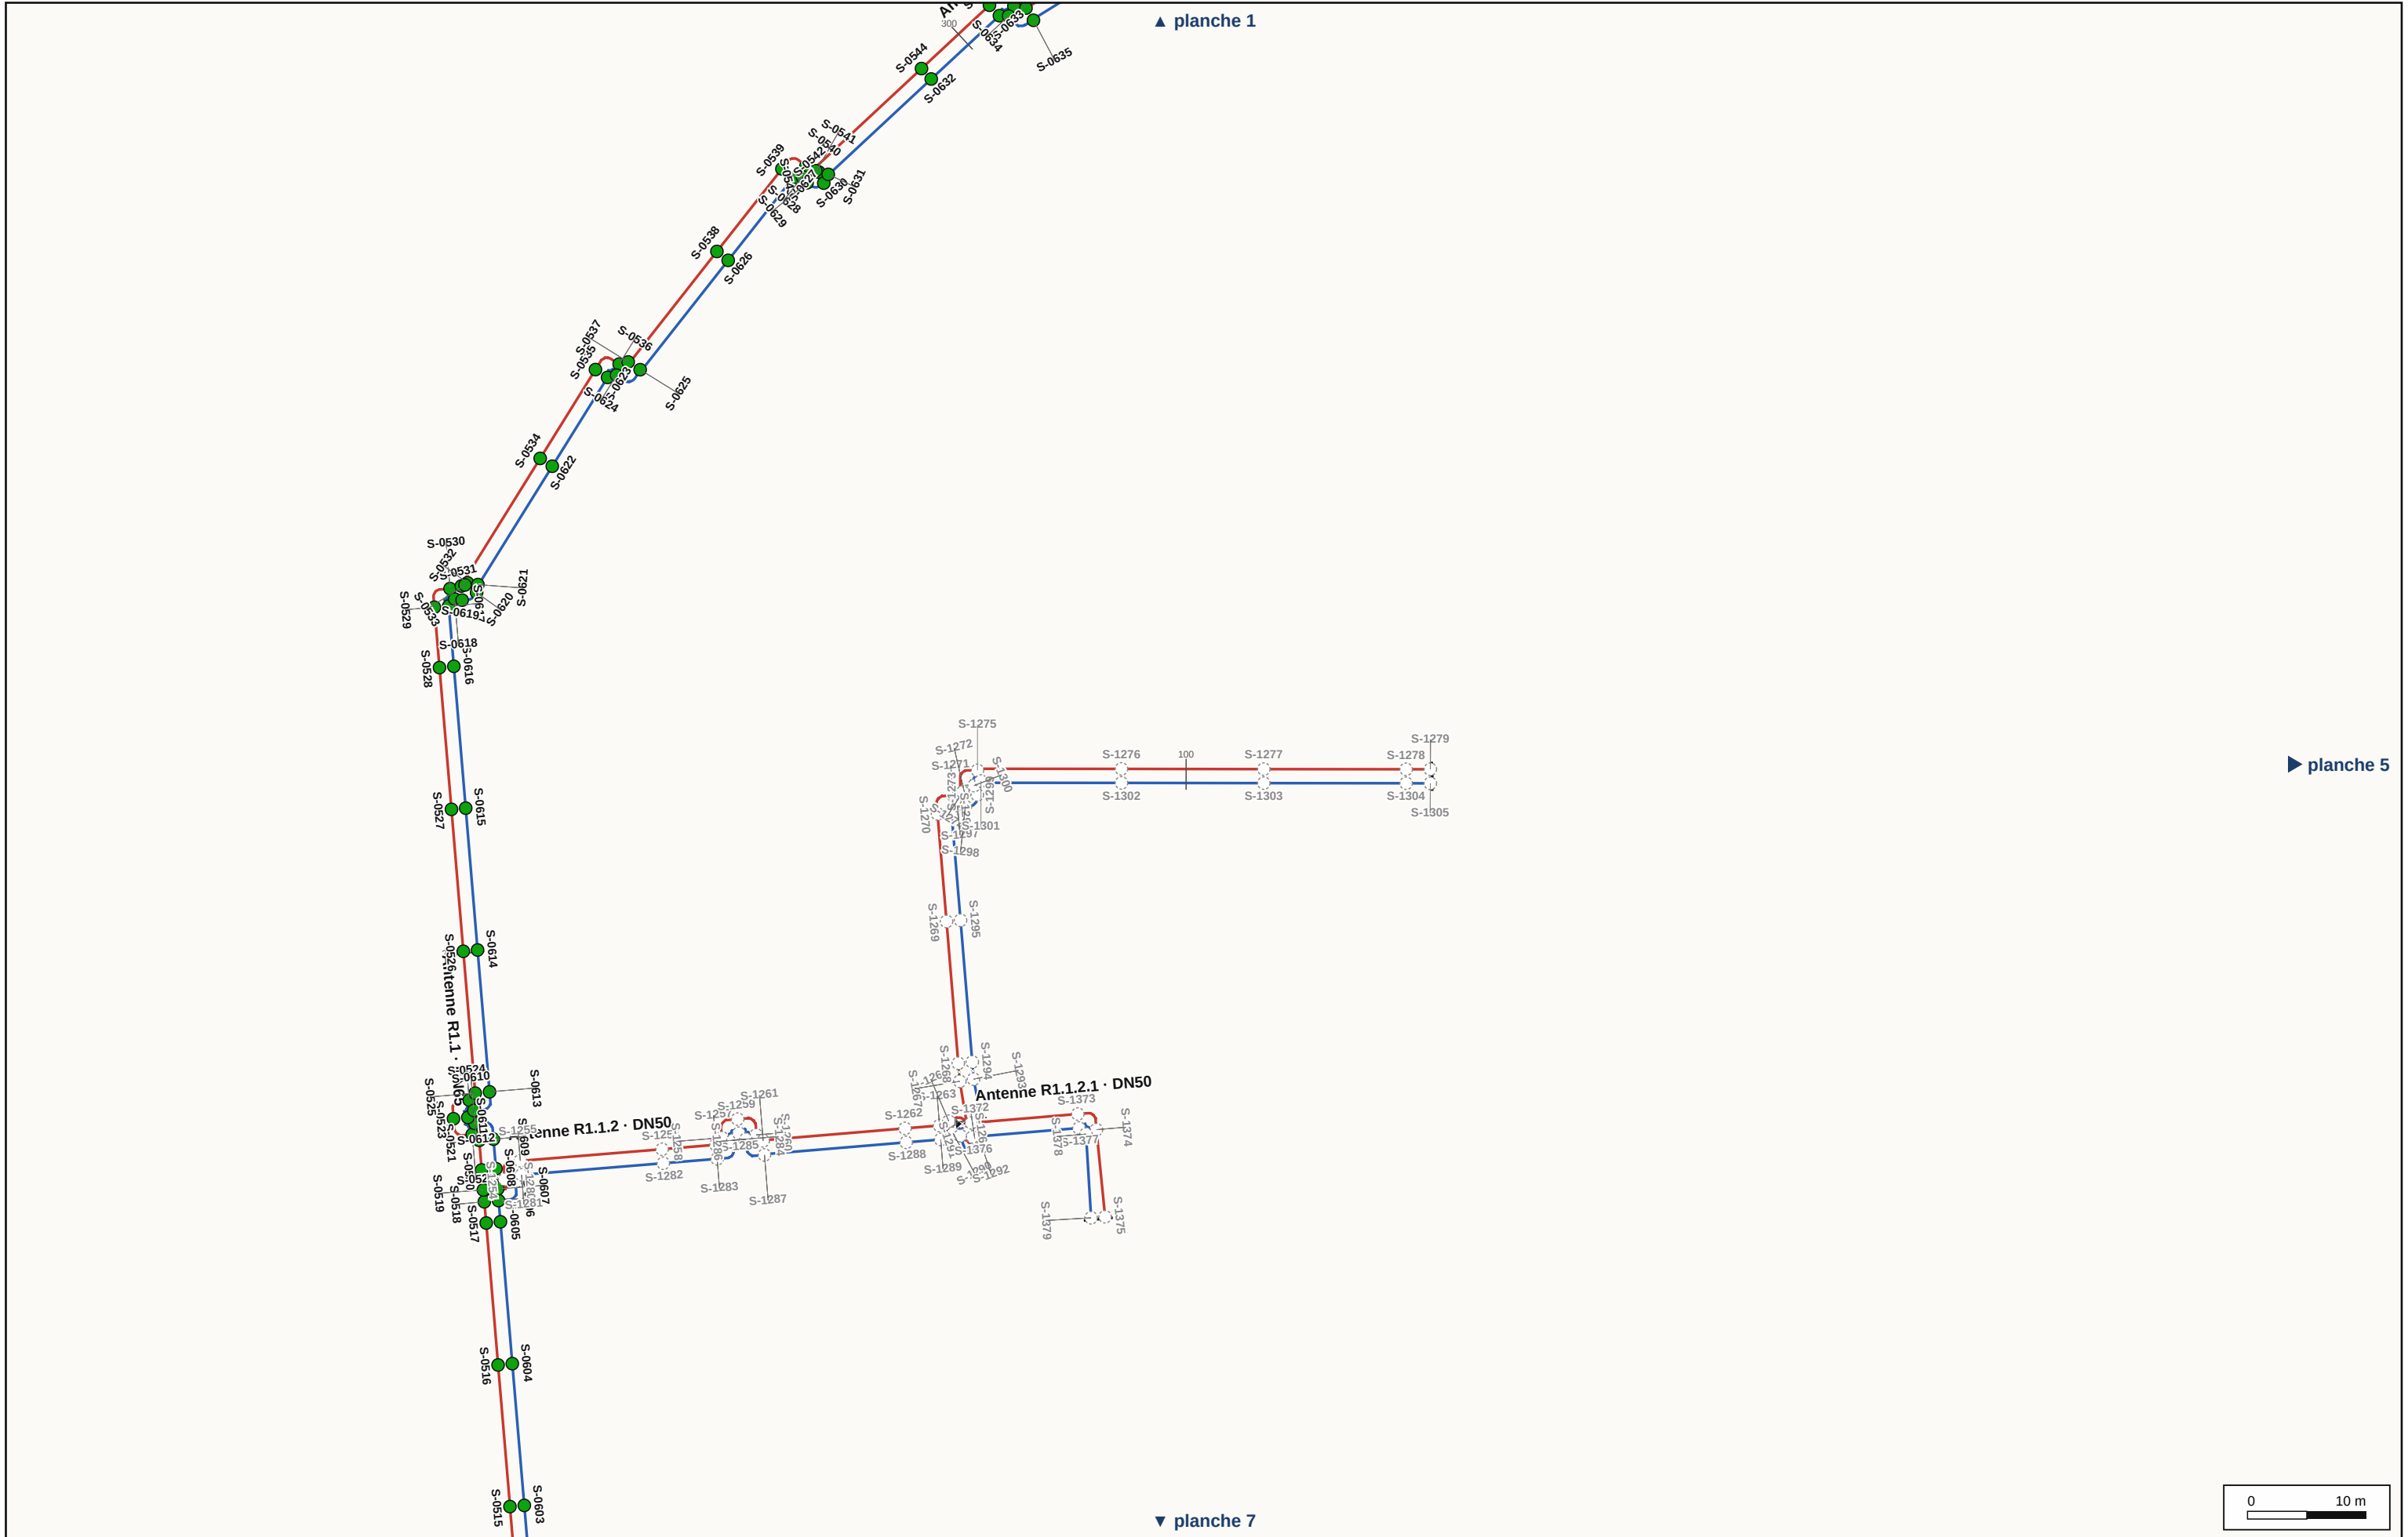

Bain-de-Bretagne — LOGSTOR (DWG calepinage)


Plan des soudures numérotées — planche 4 / 24 · échelle 1/500 sur A3

Bain-de-Bretagne — LOGSTOR (DWG calepinage) · report du carnet de soudage et manchonnage · n° = n° de soudure (pastille = advancement)
● À souder ● Soudée ● Contrôlée ● Manchonnée ● À reprendre — aller — retour ◀ vanne ▷ réduction ■ té

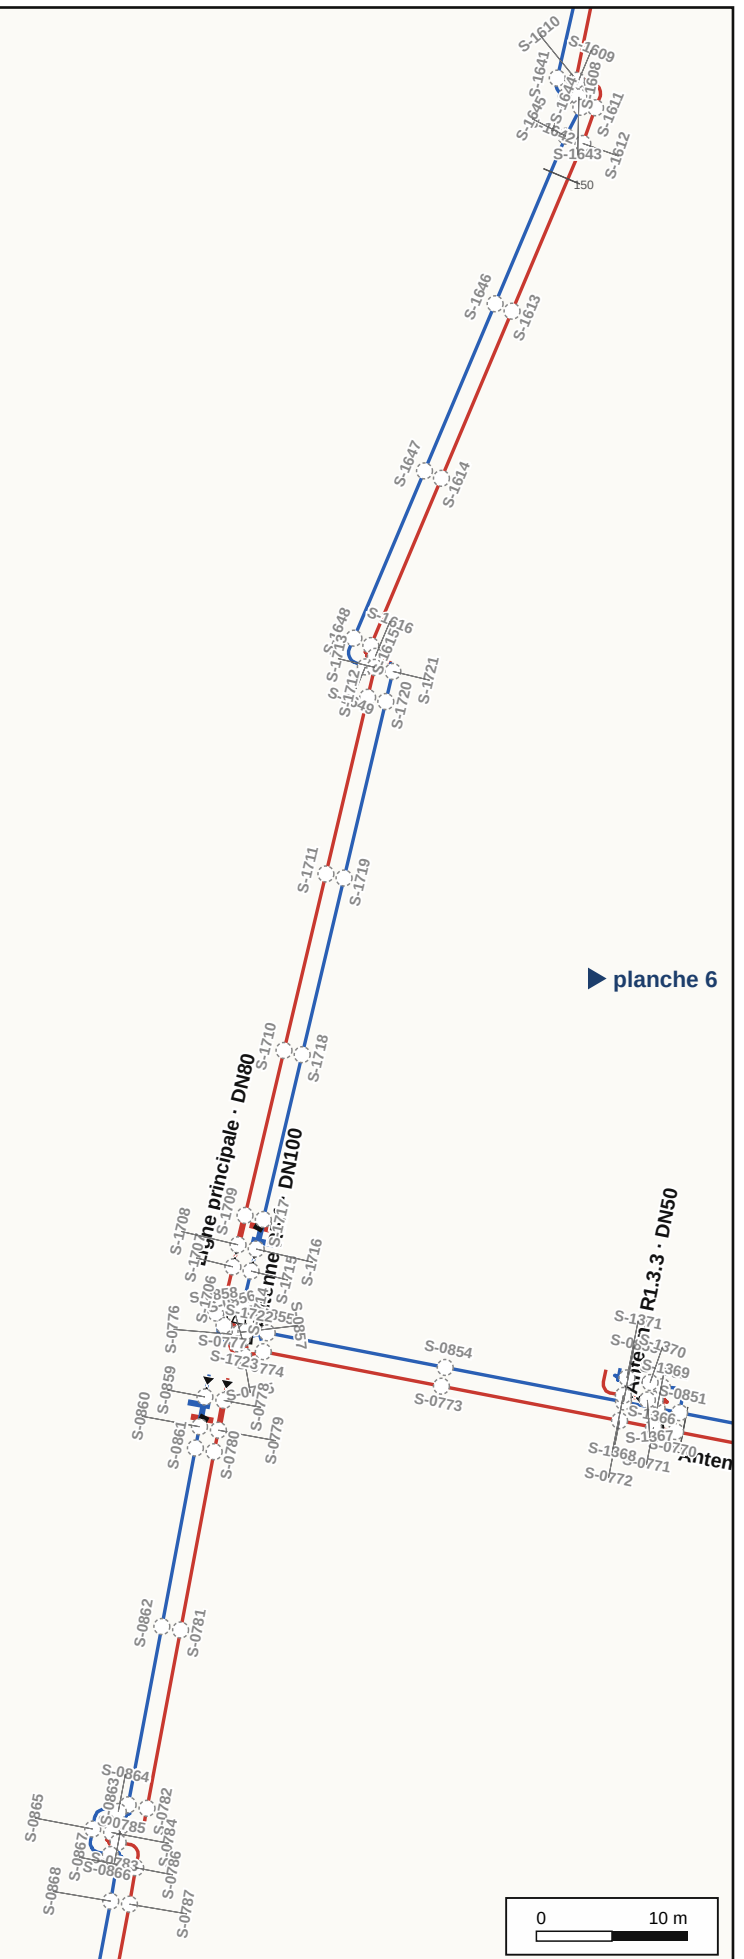


▲ planche 3

planche 5

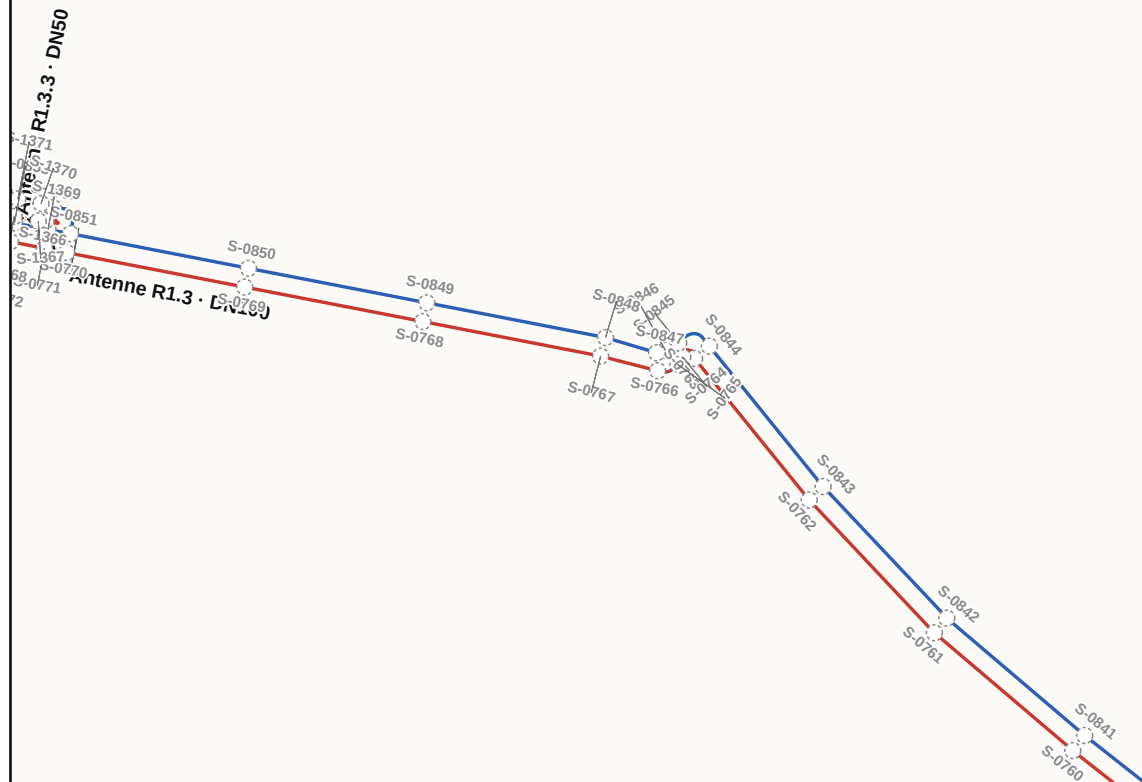

▼ planche 9

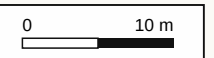

Bain-de-Bretagne — LOGSTOR (DWG calepinage)

Plan des soudures numérotées — **planche 6 / 24** · échelle 1/500 sur A3


Bain-de-Bretagne — LOGSTOR (DWG calepinage) · report du carnet de soudage et manchonnage · n° = n° de soudure (pastille = avancement)

À souder
 Soudée
 Contrôlée
 Manchonnée
 À reprendre
 aller
 retour
 vanne
 réduction
 té

Planche 6 / 24

édité le 07/10/2026 par Ethan L.

TRACÉ / RCU-COMPAGNON

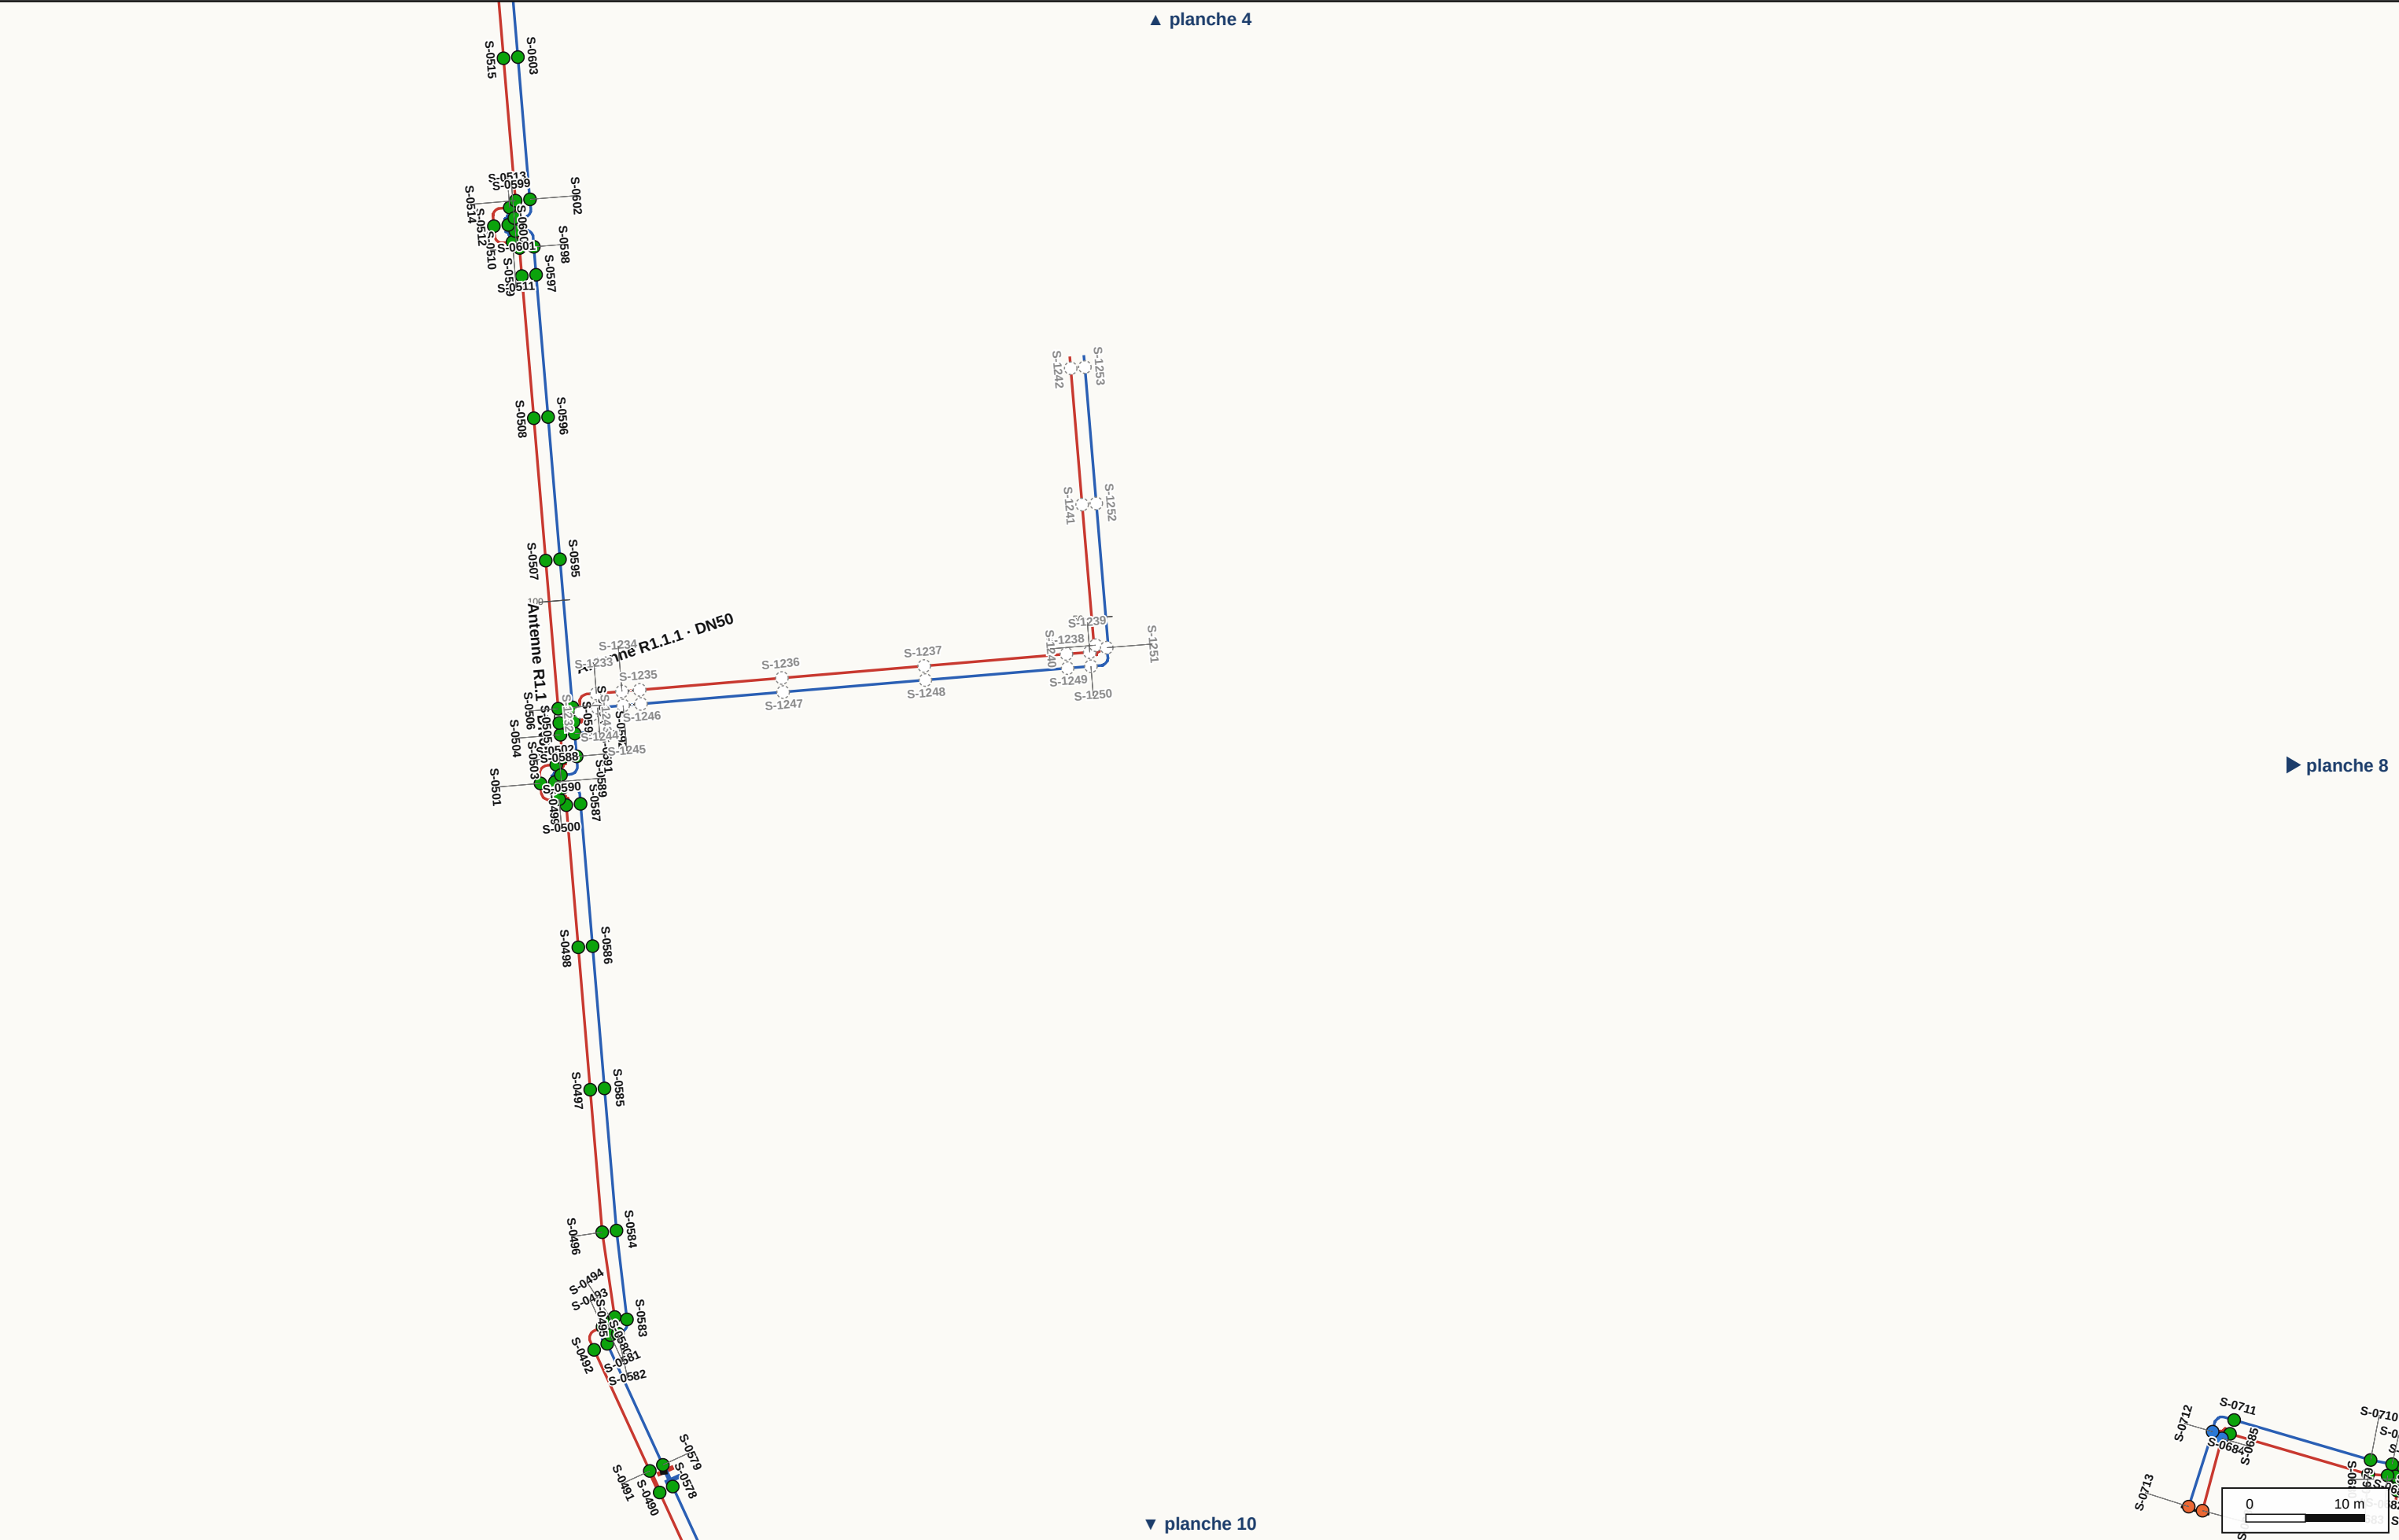





Bain-de-Bretagne — LOGSTOR (DWG calepinage)

Plan des soudures numérotées — planche 11 / 24 · échelle 1/500 sur A3

Bain-de-Bretagne — LOGSTOR (DWG calepinage) · report du carnet de soudage et manchonnage · n° = n° de soudure (pastille = advancement)
● À souder ● Soudée ● Contrôlée ● Manchonnée ● À reprendre — aller — retour — vanne — réduction — té



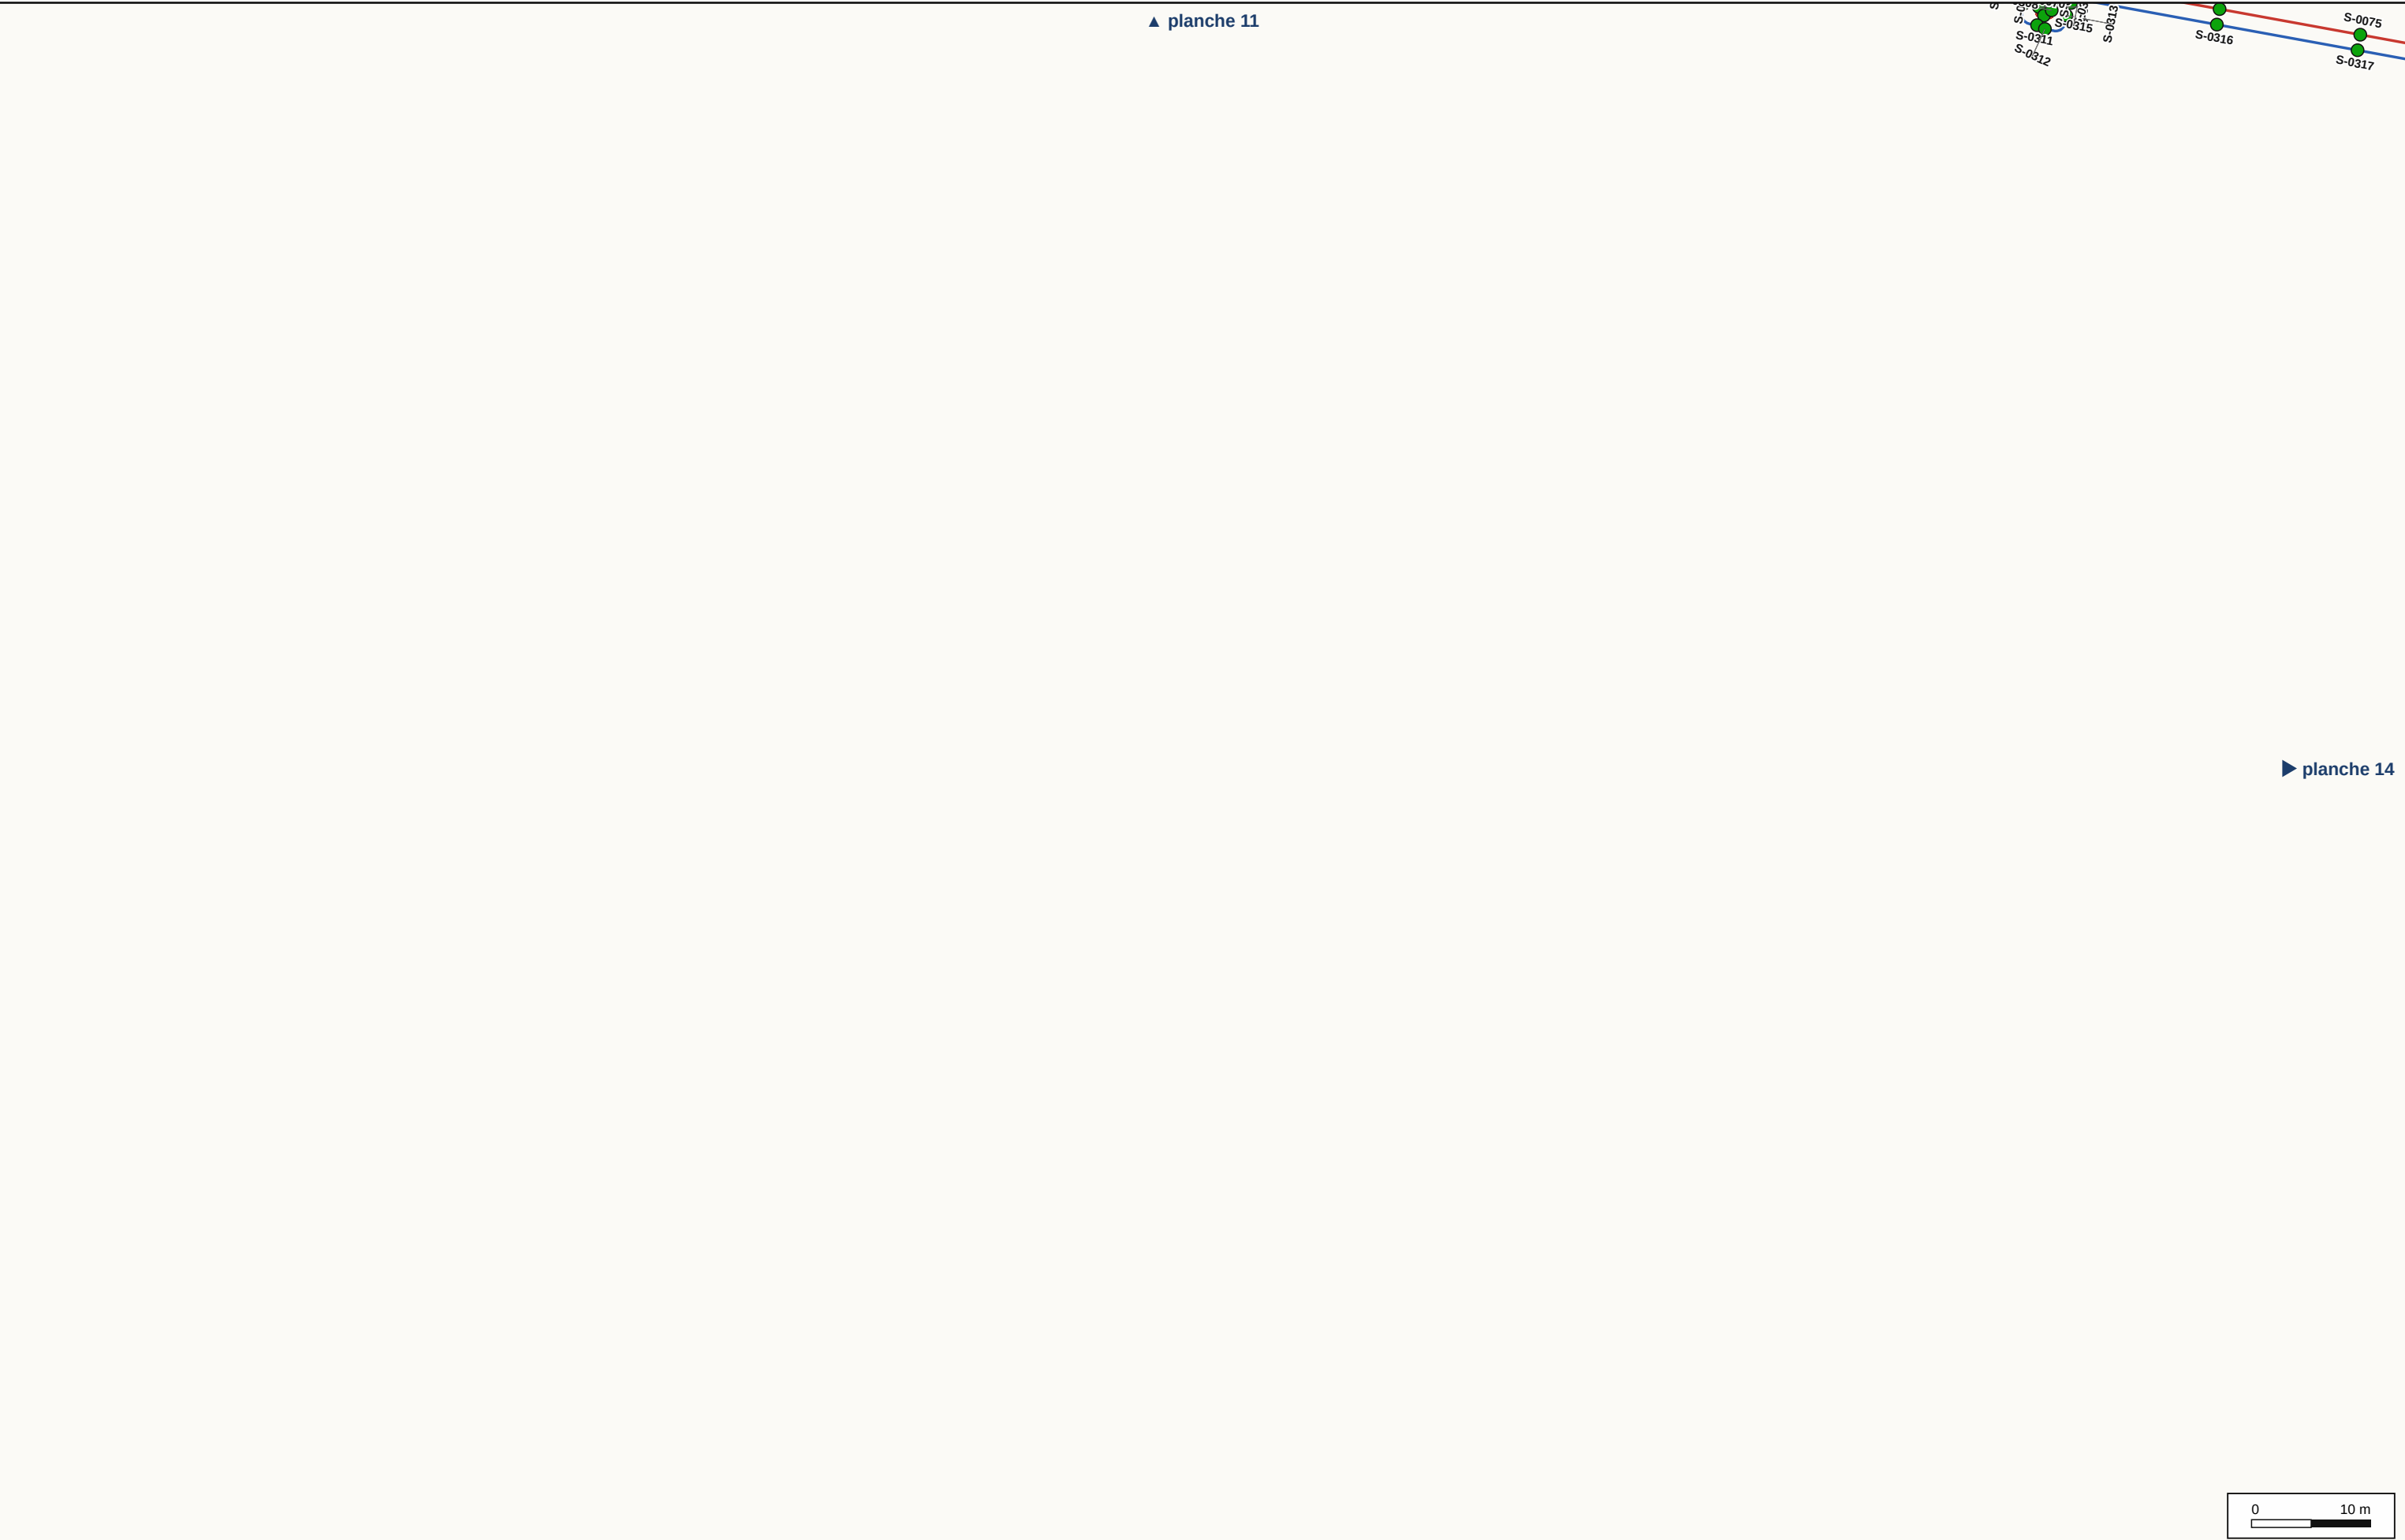

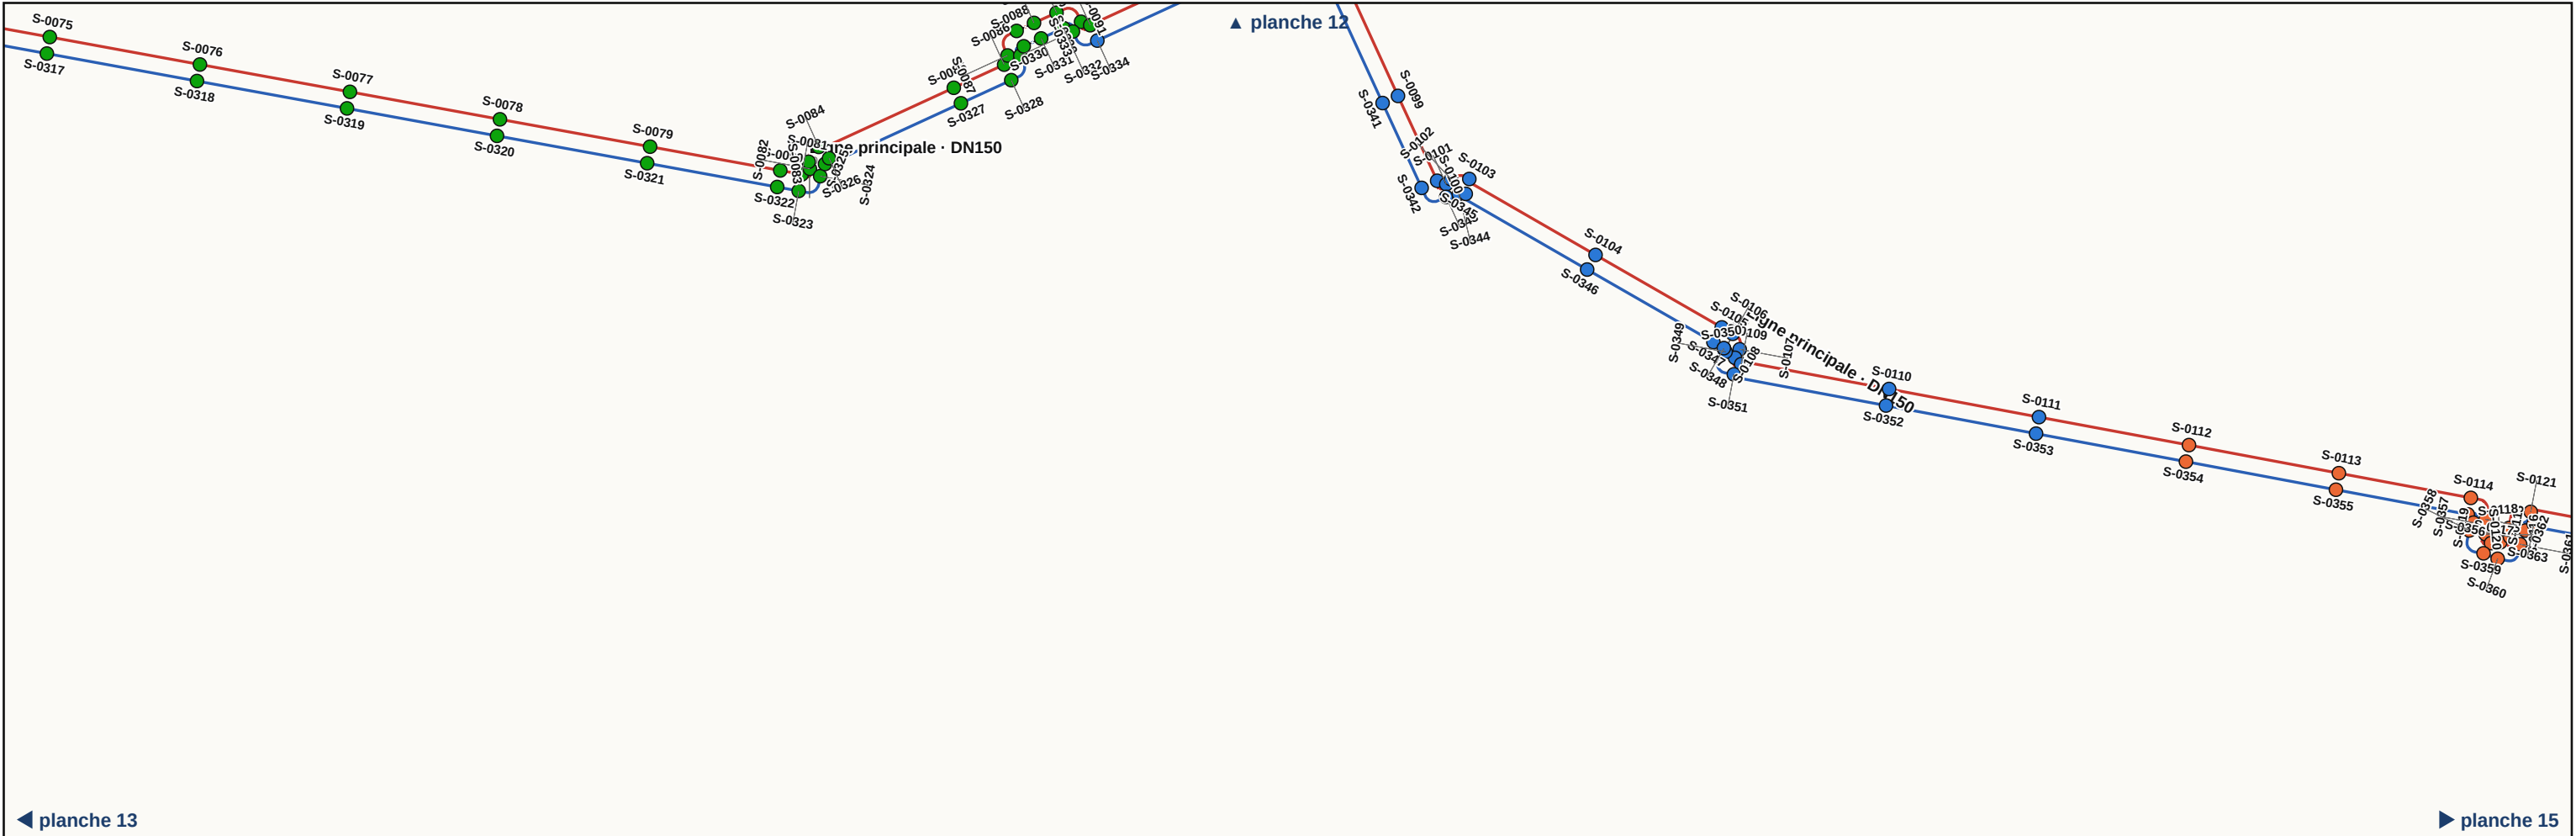


Bain-de-Bretagne — LOGSTOR (DWG calepinage)

Plan des soudures numérotées — planche 14 / 24 · échelle 1/500 sur A3

Bain-de-Bretagne — LOGSTOR (DWG calepinage) · report du carnet de soudage et manchonnage · n° = n° de soudure (pastille = advancement)


● À souder ● Soudée ● Contrôlée ● Manchonnée ● À reprendre — aller — retour ◀ vanne ▷ réduction ■ té

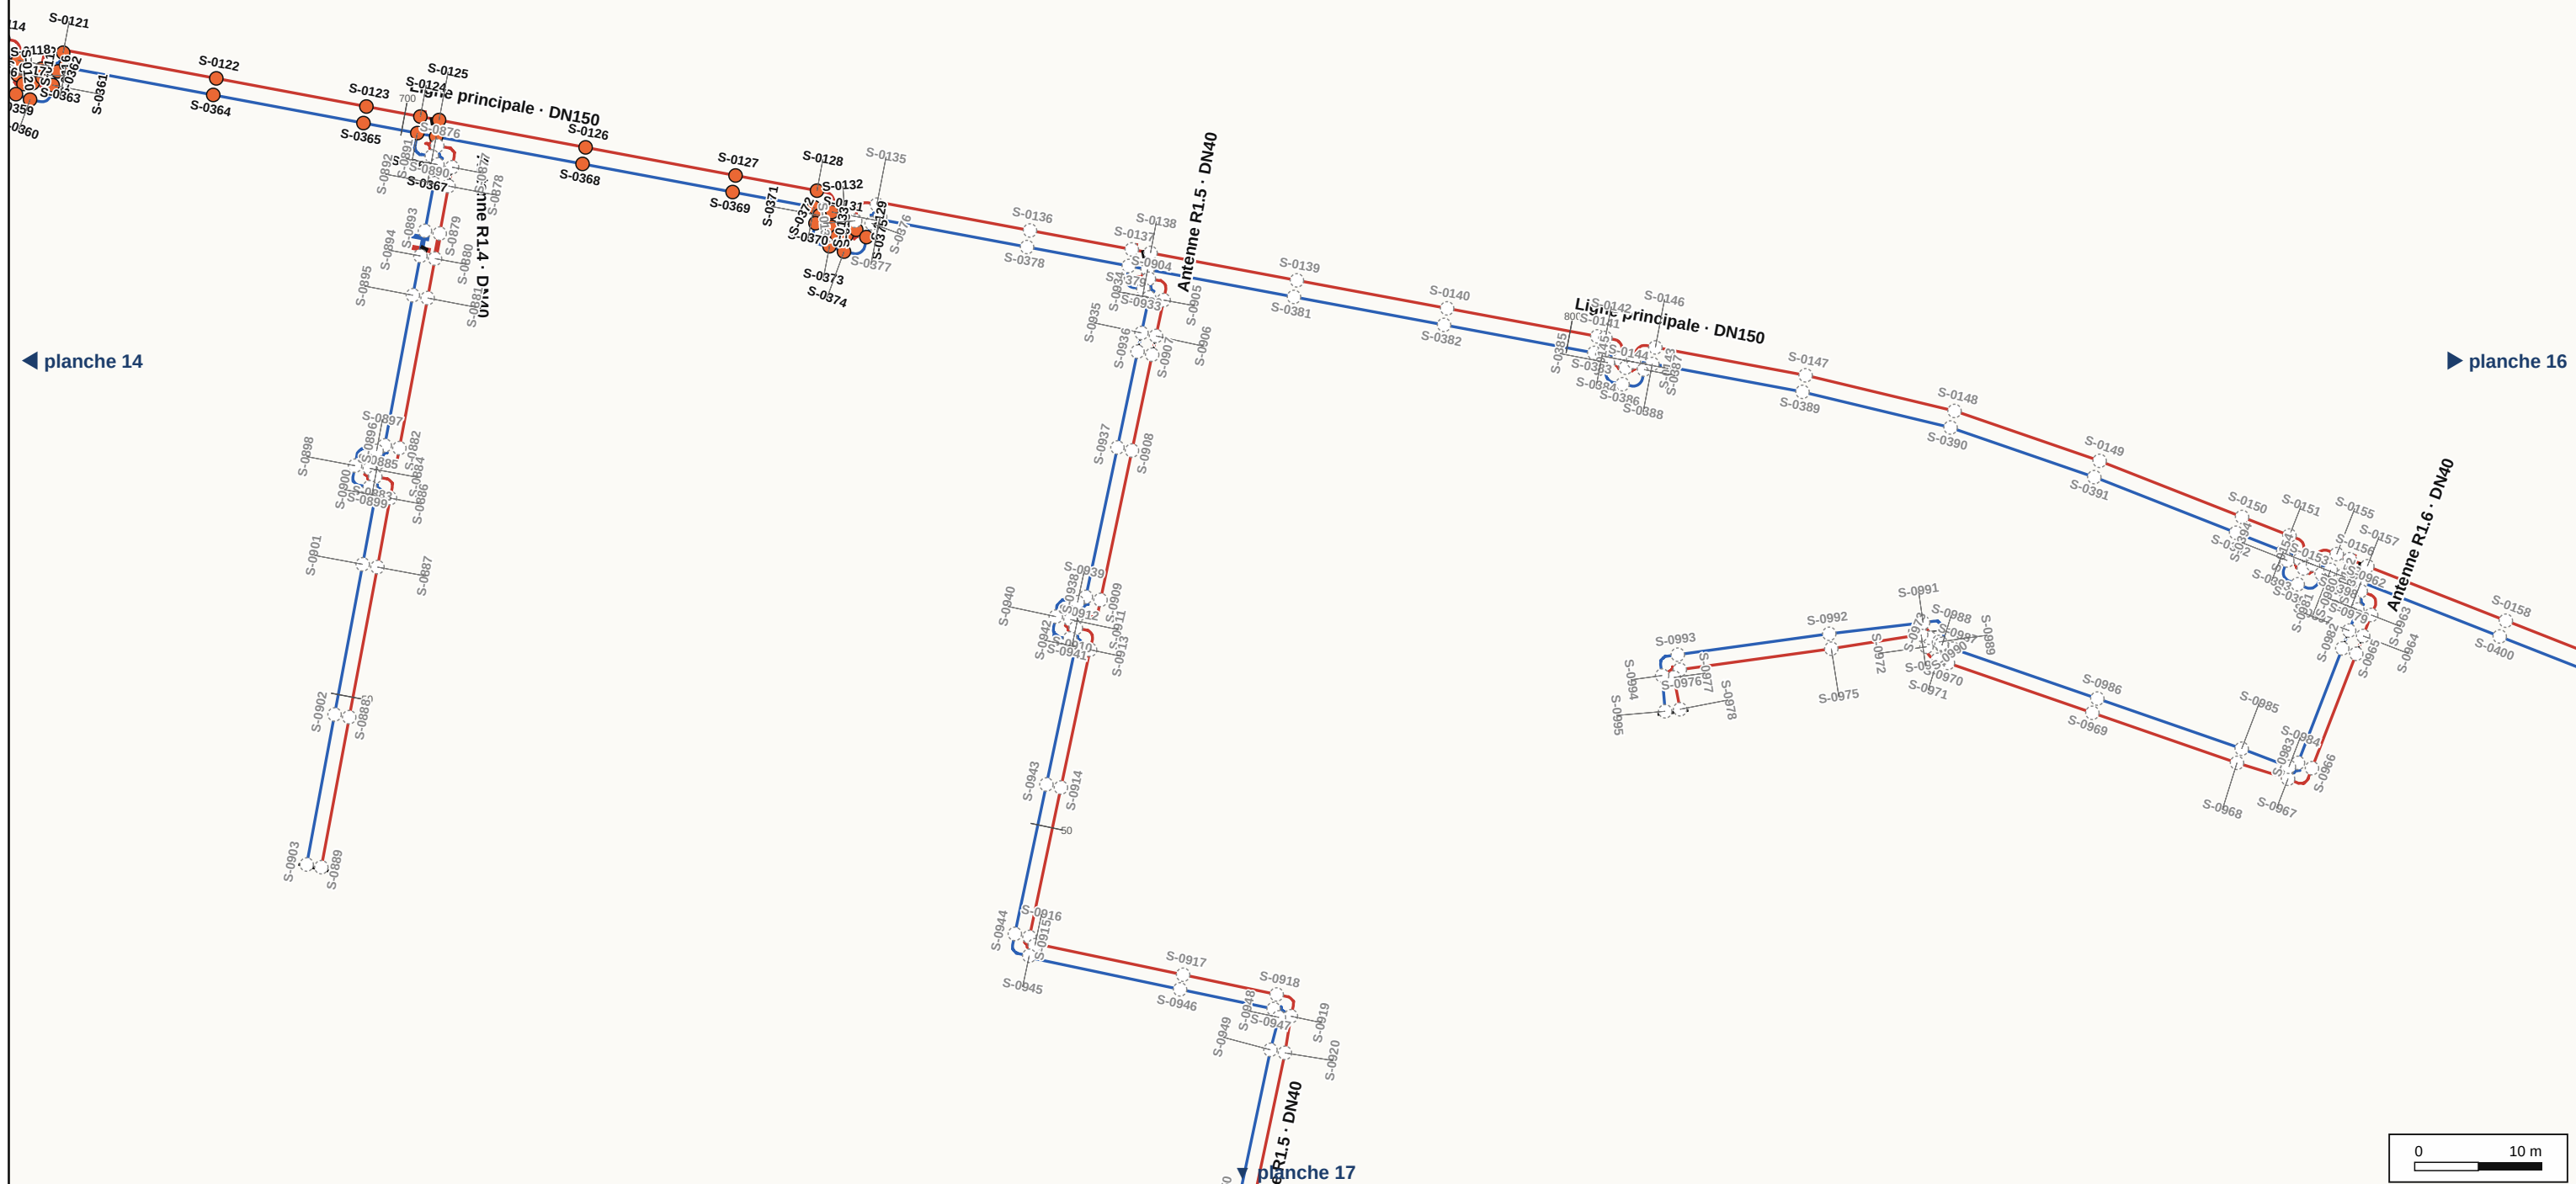

Bain-de-Bretagne — LOGSTOR (DWG calepinage) · report du carnet de soudage et manchonnage · n° = n° de soudure (pastille = avancement)

● À souder ● Soudée ● Contrôlée ● Manchonnée ● À reprendre — aller — retour ◀ vanne ▽ réduction ■ té

◀ planche 15

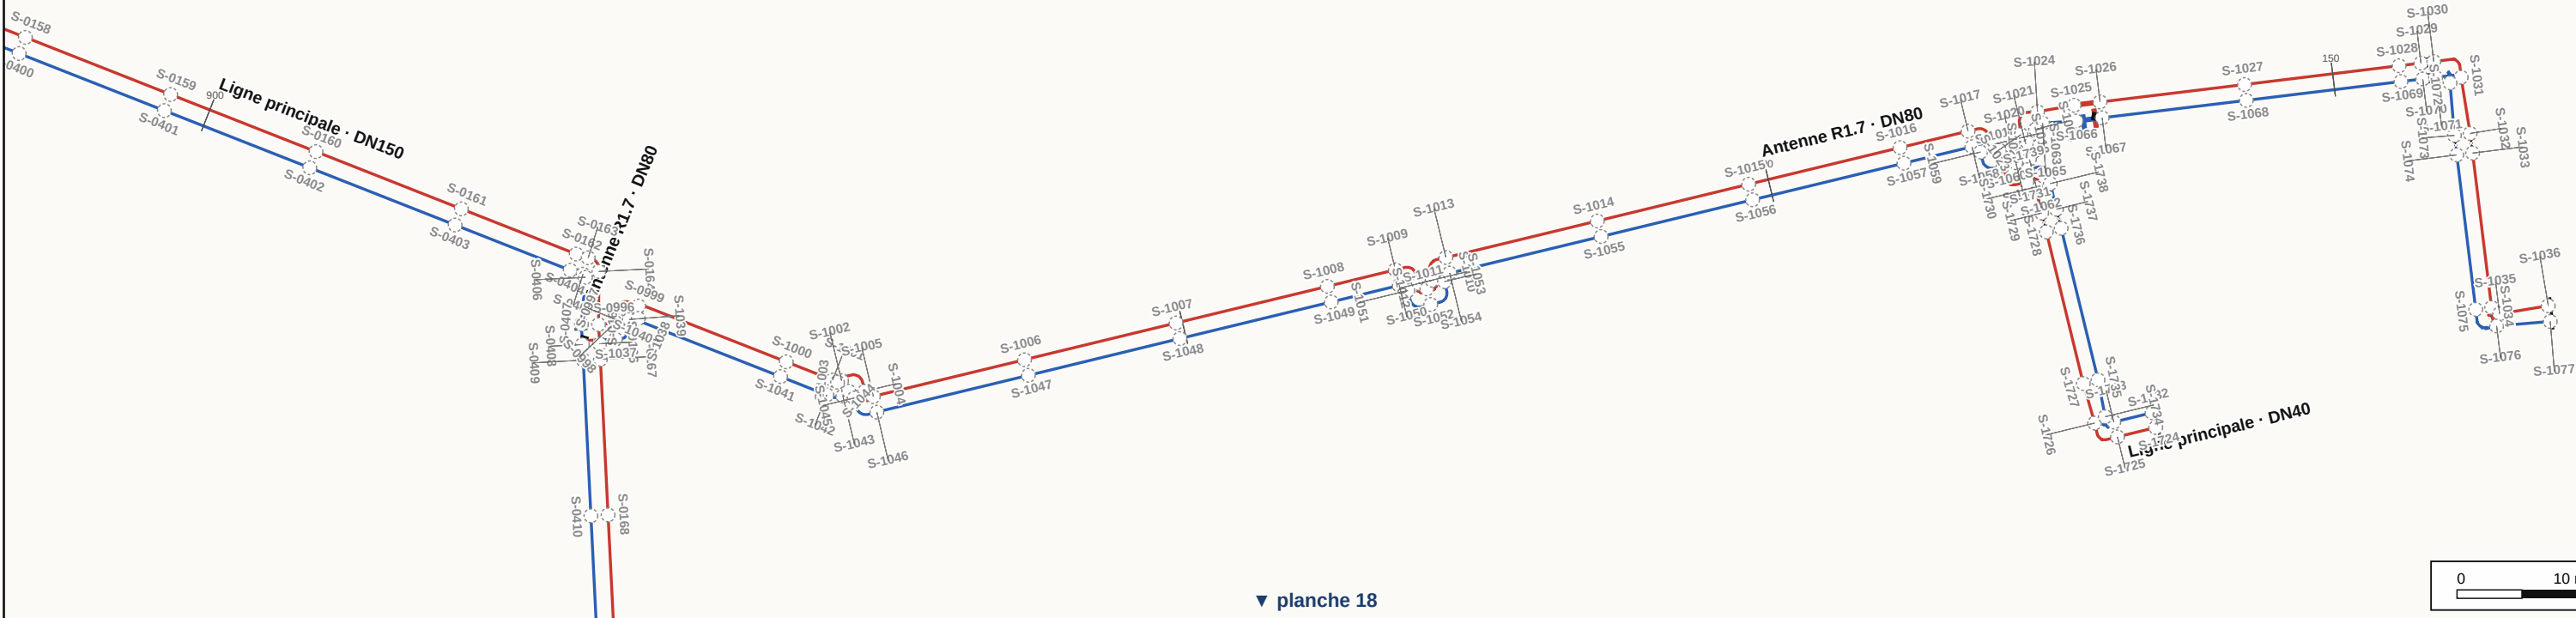

▼ planche 18

Bain-de-Bretagne — LOGSTOR (DWG calepinage)


Plan des soudures numérotées — planche 16 / 24 · échelle 1/500 sur A3

Bain-de-Bretagne — LOGSTOR (DWG calepinage) · report du carnet de soudage et manchonnage · n° = n° de soudure (pastille = avancement)

● À souder ● Soudée ● Contrôlée ● Manchonnée ● À reprendre

aller retour

vanne réduction té

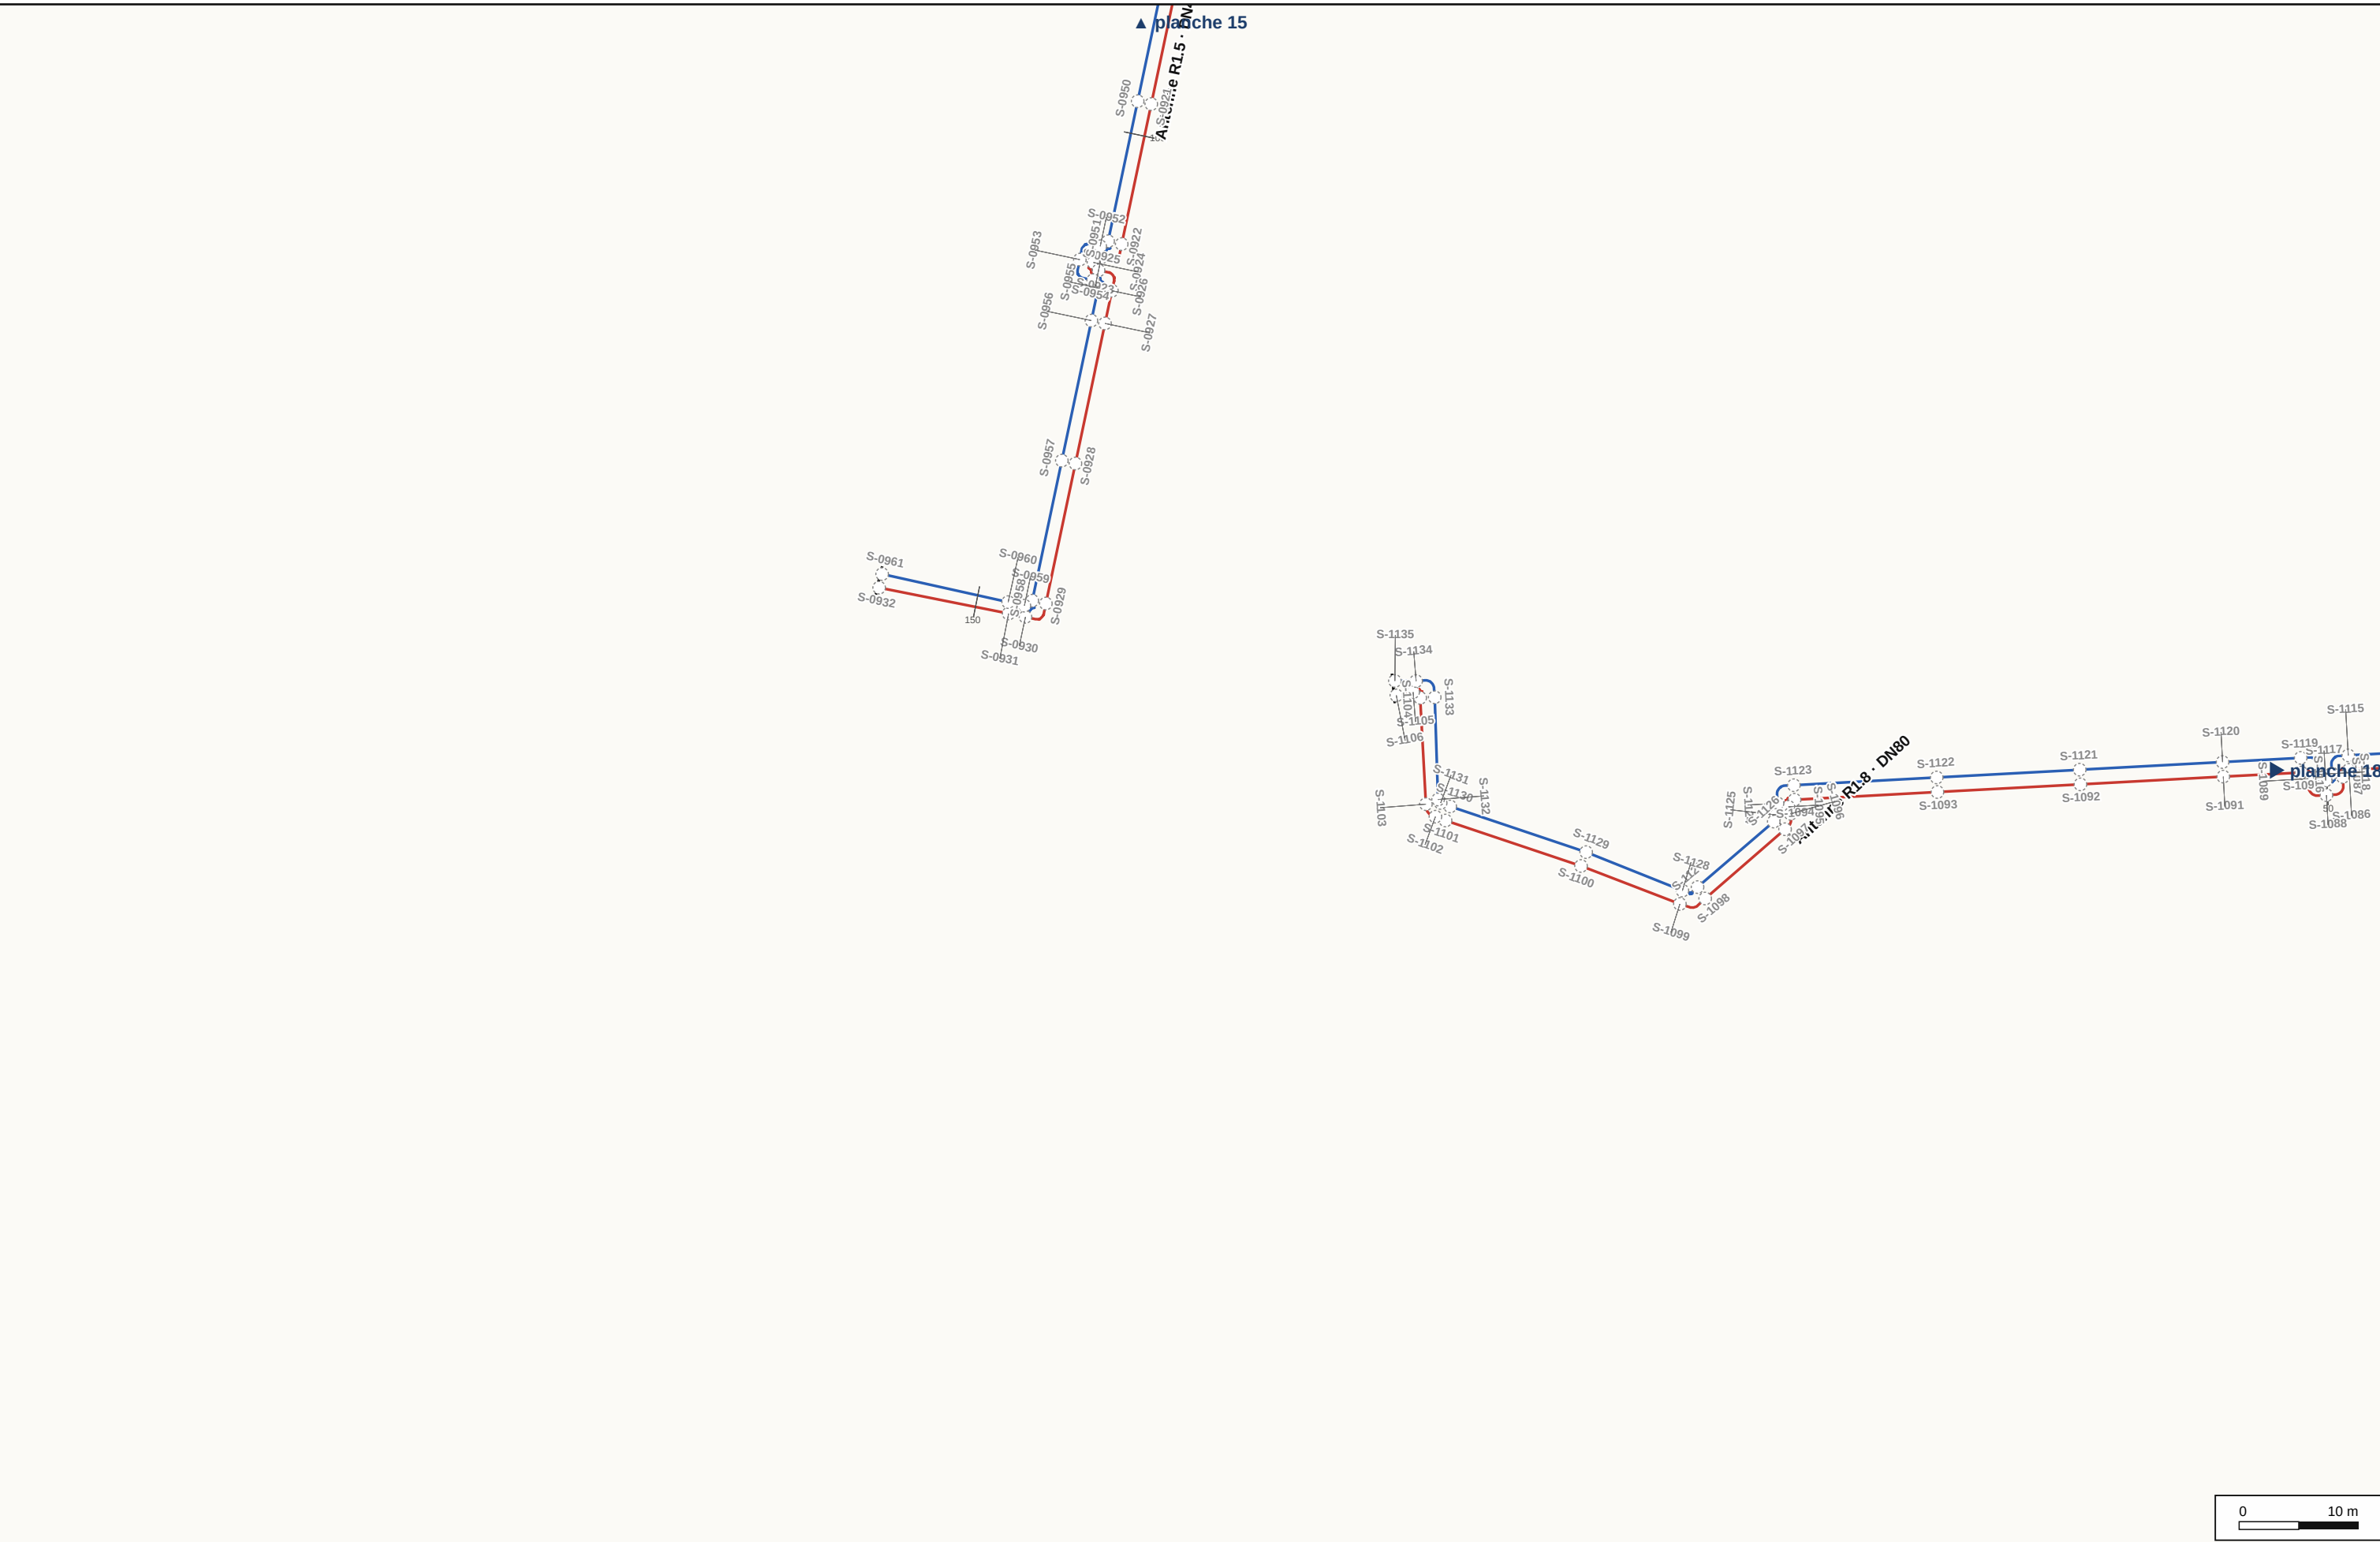


Bain-de-Bretagne — LOGSTOR (DWG calepinage)

Plan des soudures numérotées — planche 17 / 24 · échelle 1/500 sur A3

Bain-de-Bretagne — LOGSTOR (DWG calepinage) · report du carnet de soudage et manchonnage · n° = n° de soudure (pastille = avancement)

● À souder ● Soudée ● Contrôlée ● Manchonnée ● À reprendre — aller — retour ◀ vanne ▷ réduction ■ té

▲ planche 16

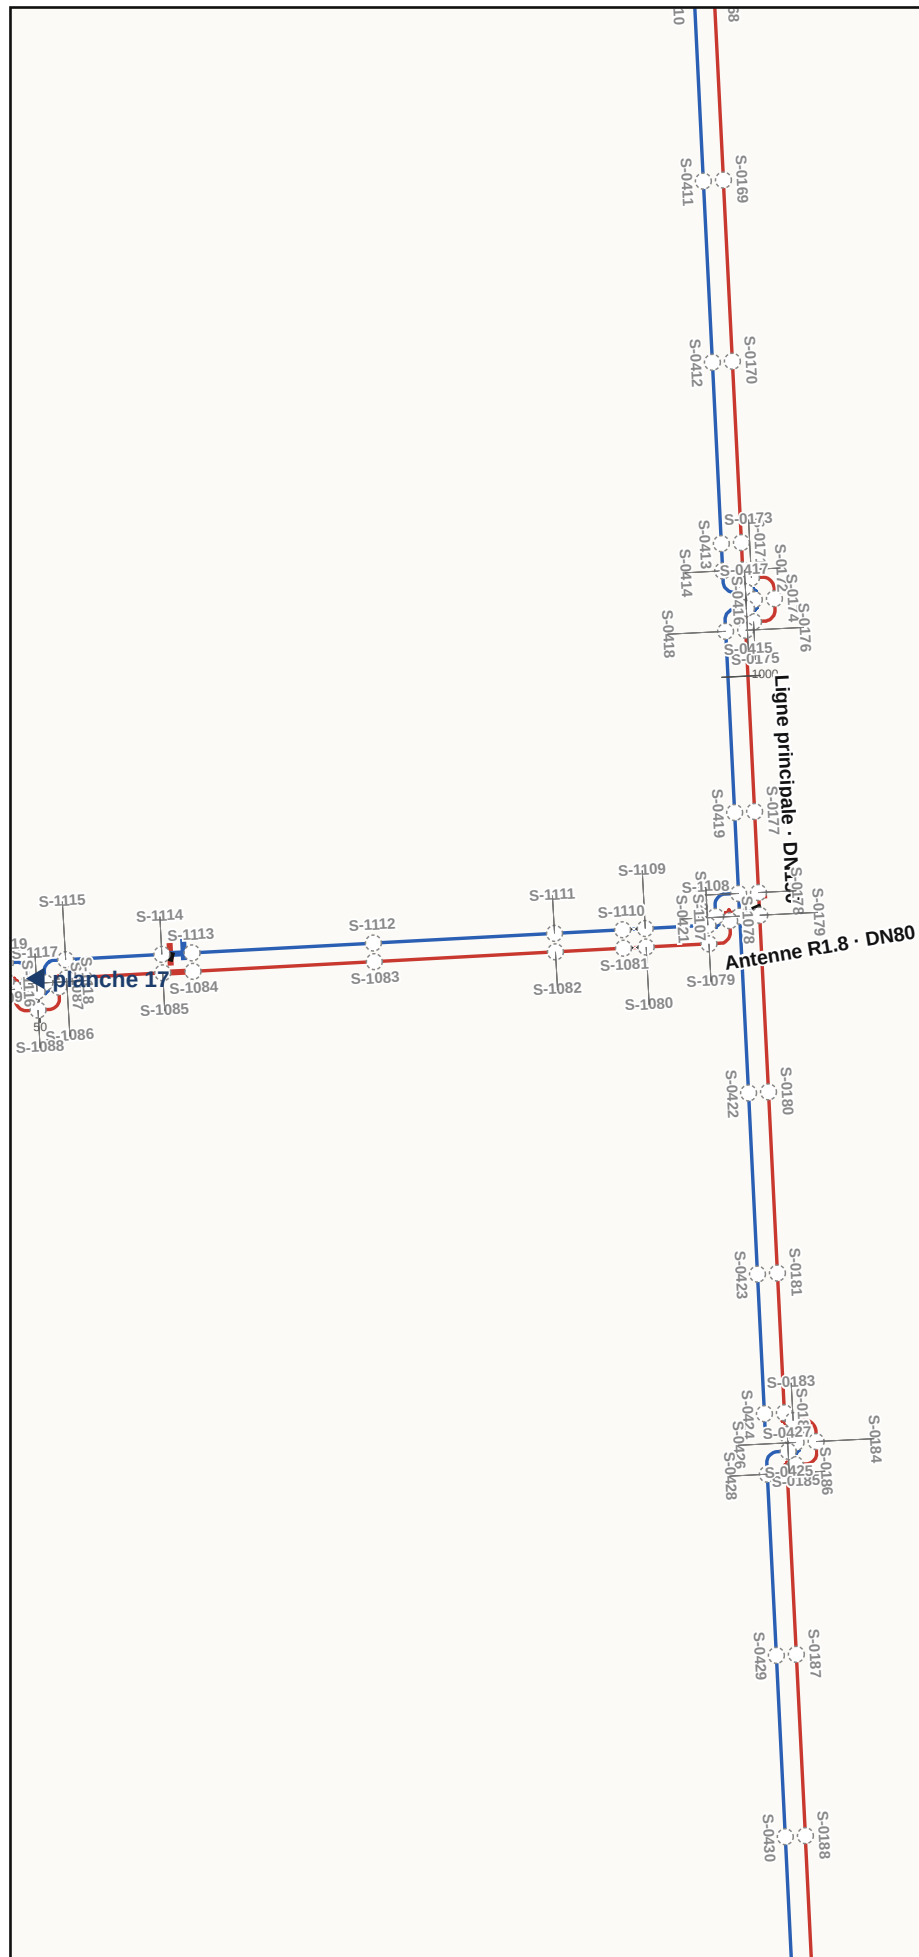

▼ planche 19



Bain-de-Bretagne — LOGSTOR (DWG calepinage)

Plan des soudures numérotées — **planche 18 / 24** · échelle 1/500 sur A3

Bain-de-Bretagne — LOGSTOR (DWG calepinage) · report du carnet de soudage et manchonnage · n° = n° de soudure (pastille = avancement)

● À souder
 ● Soudée
 ● Contrôlée
 ● Manchonnée
 ● À reprendre
 — aller
 — retour
 ◀▶ vanne

Planche 18 / 24

édité le 07/10/2026 par Ethan L.

TRACÉ / RCU-COMPAGNON



Planche 19 / 24

édité le 07/10/2026 par Ethan L.

TRACÉ / RCU-COMPAGNON

TRACÉ / RCU-COMPAGNON



Bain-de-Bretagne — LOGSTOR (DWG calepinage) · report du carnet de soudage et manchonnage · n° = n° de soudure (pastille = avancement)

● À souder
 ● Soudée
 ● Contrôlée
 ● Manchonnée
 ● À reprendre
 — aller
 — retour
 ◀▶ vanne

TRACÉ / RCU-COMPAGNON




Planche 21 / 24

édité le 07/10/2026 par Ethan L.


TRACÉ / RCU-COMPAGNON

TRACÉ / RCU-COMPAGNON

▲ planche 21

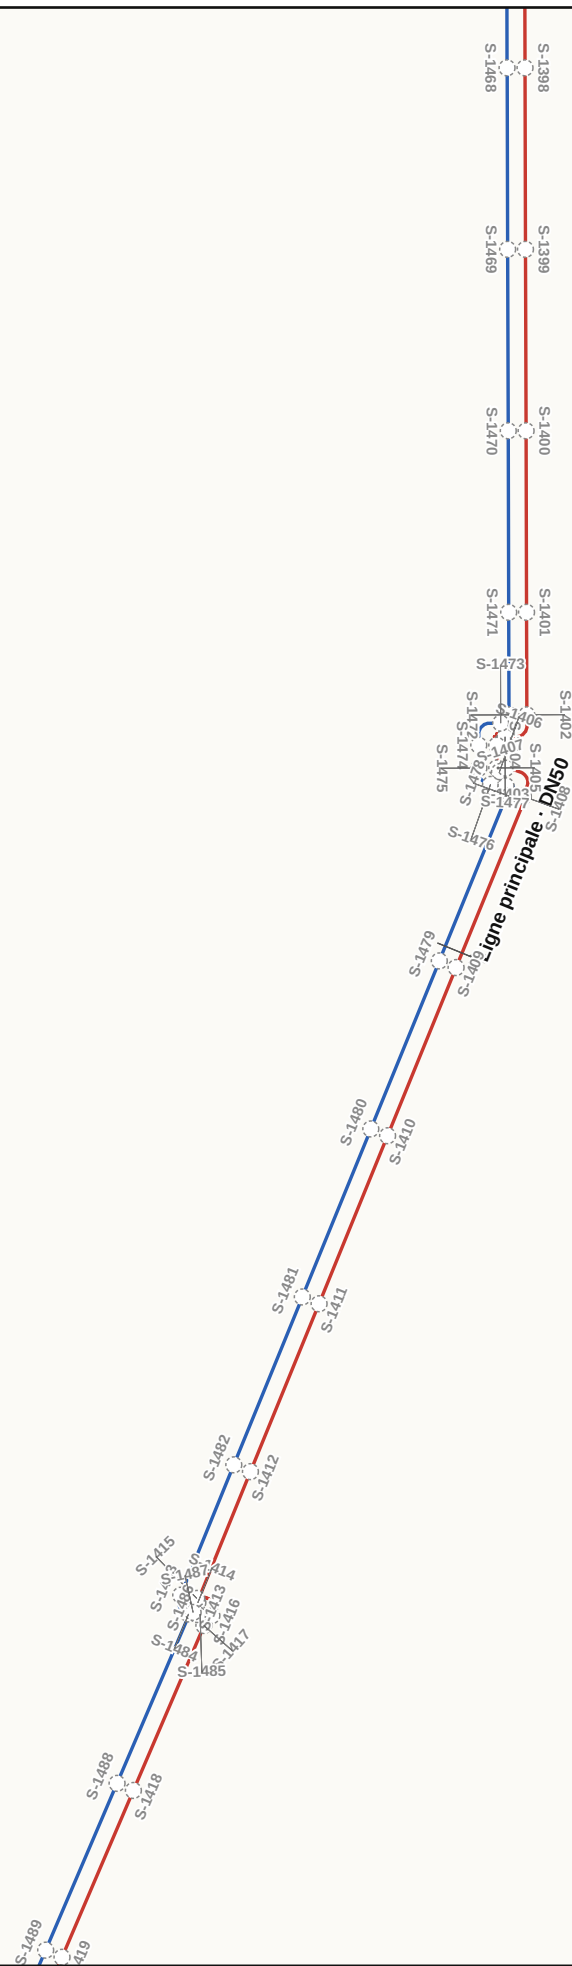

▼ planche 23

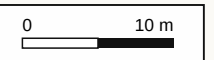

Bain-de-Bretagne — LOGSTOR (DWG calepinage)

Plan des soudures numérotées — **planche 22 / 24** · échelle 1/500 sur A3

Bain-de-Bretagne — LOGSTOR (DWG calepinage) · report du carnet de soudage et manchonnage · n° = n° de soudure (pastille = avancement)


● À souder
 ● Soudée
 ● Contrôlée
 ● Manchonnée
 ● À reprendre
 — aller
 — retour
 ◀▶ vanne

À souder
 Soudée
 Contrôlée
 Manchonnée
 À reprendre
 aller
 retour
 vanne
 réduction
 té

Planche 22 / 24

édité le 07/10/2026 par Ethan L.



TRACÉ / RCU-COMPAGNON

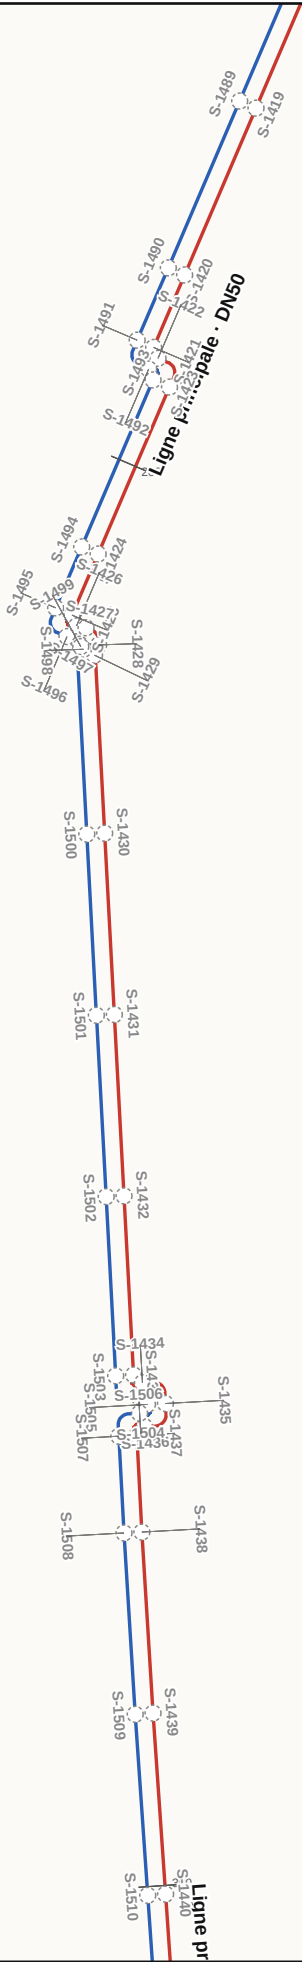

Bain-de-Bretagne — LOGSTOR (DWG calepinage)

Plan des soudures numérotées — planche 23 / 24 · échelle 1/500 sur A3

Bain-de-Bretagne — LOGSTOR (DWG calepinage) · report du carnet de soudage et manchonnage · n° = n° de soudure (pastille = advancement)
● À souder ● Soudée ● Contrôlée ● Manchonnée ● À reprendre — aller — retour — vanne — réduction — té

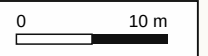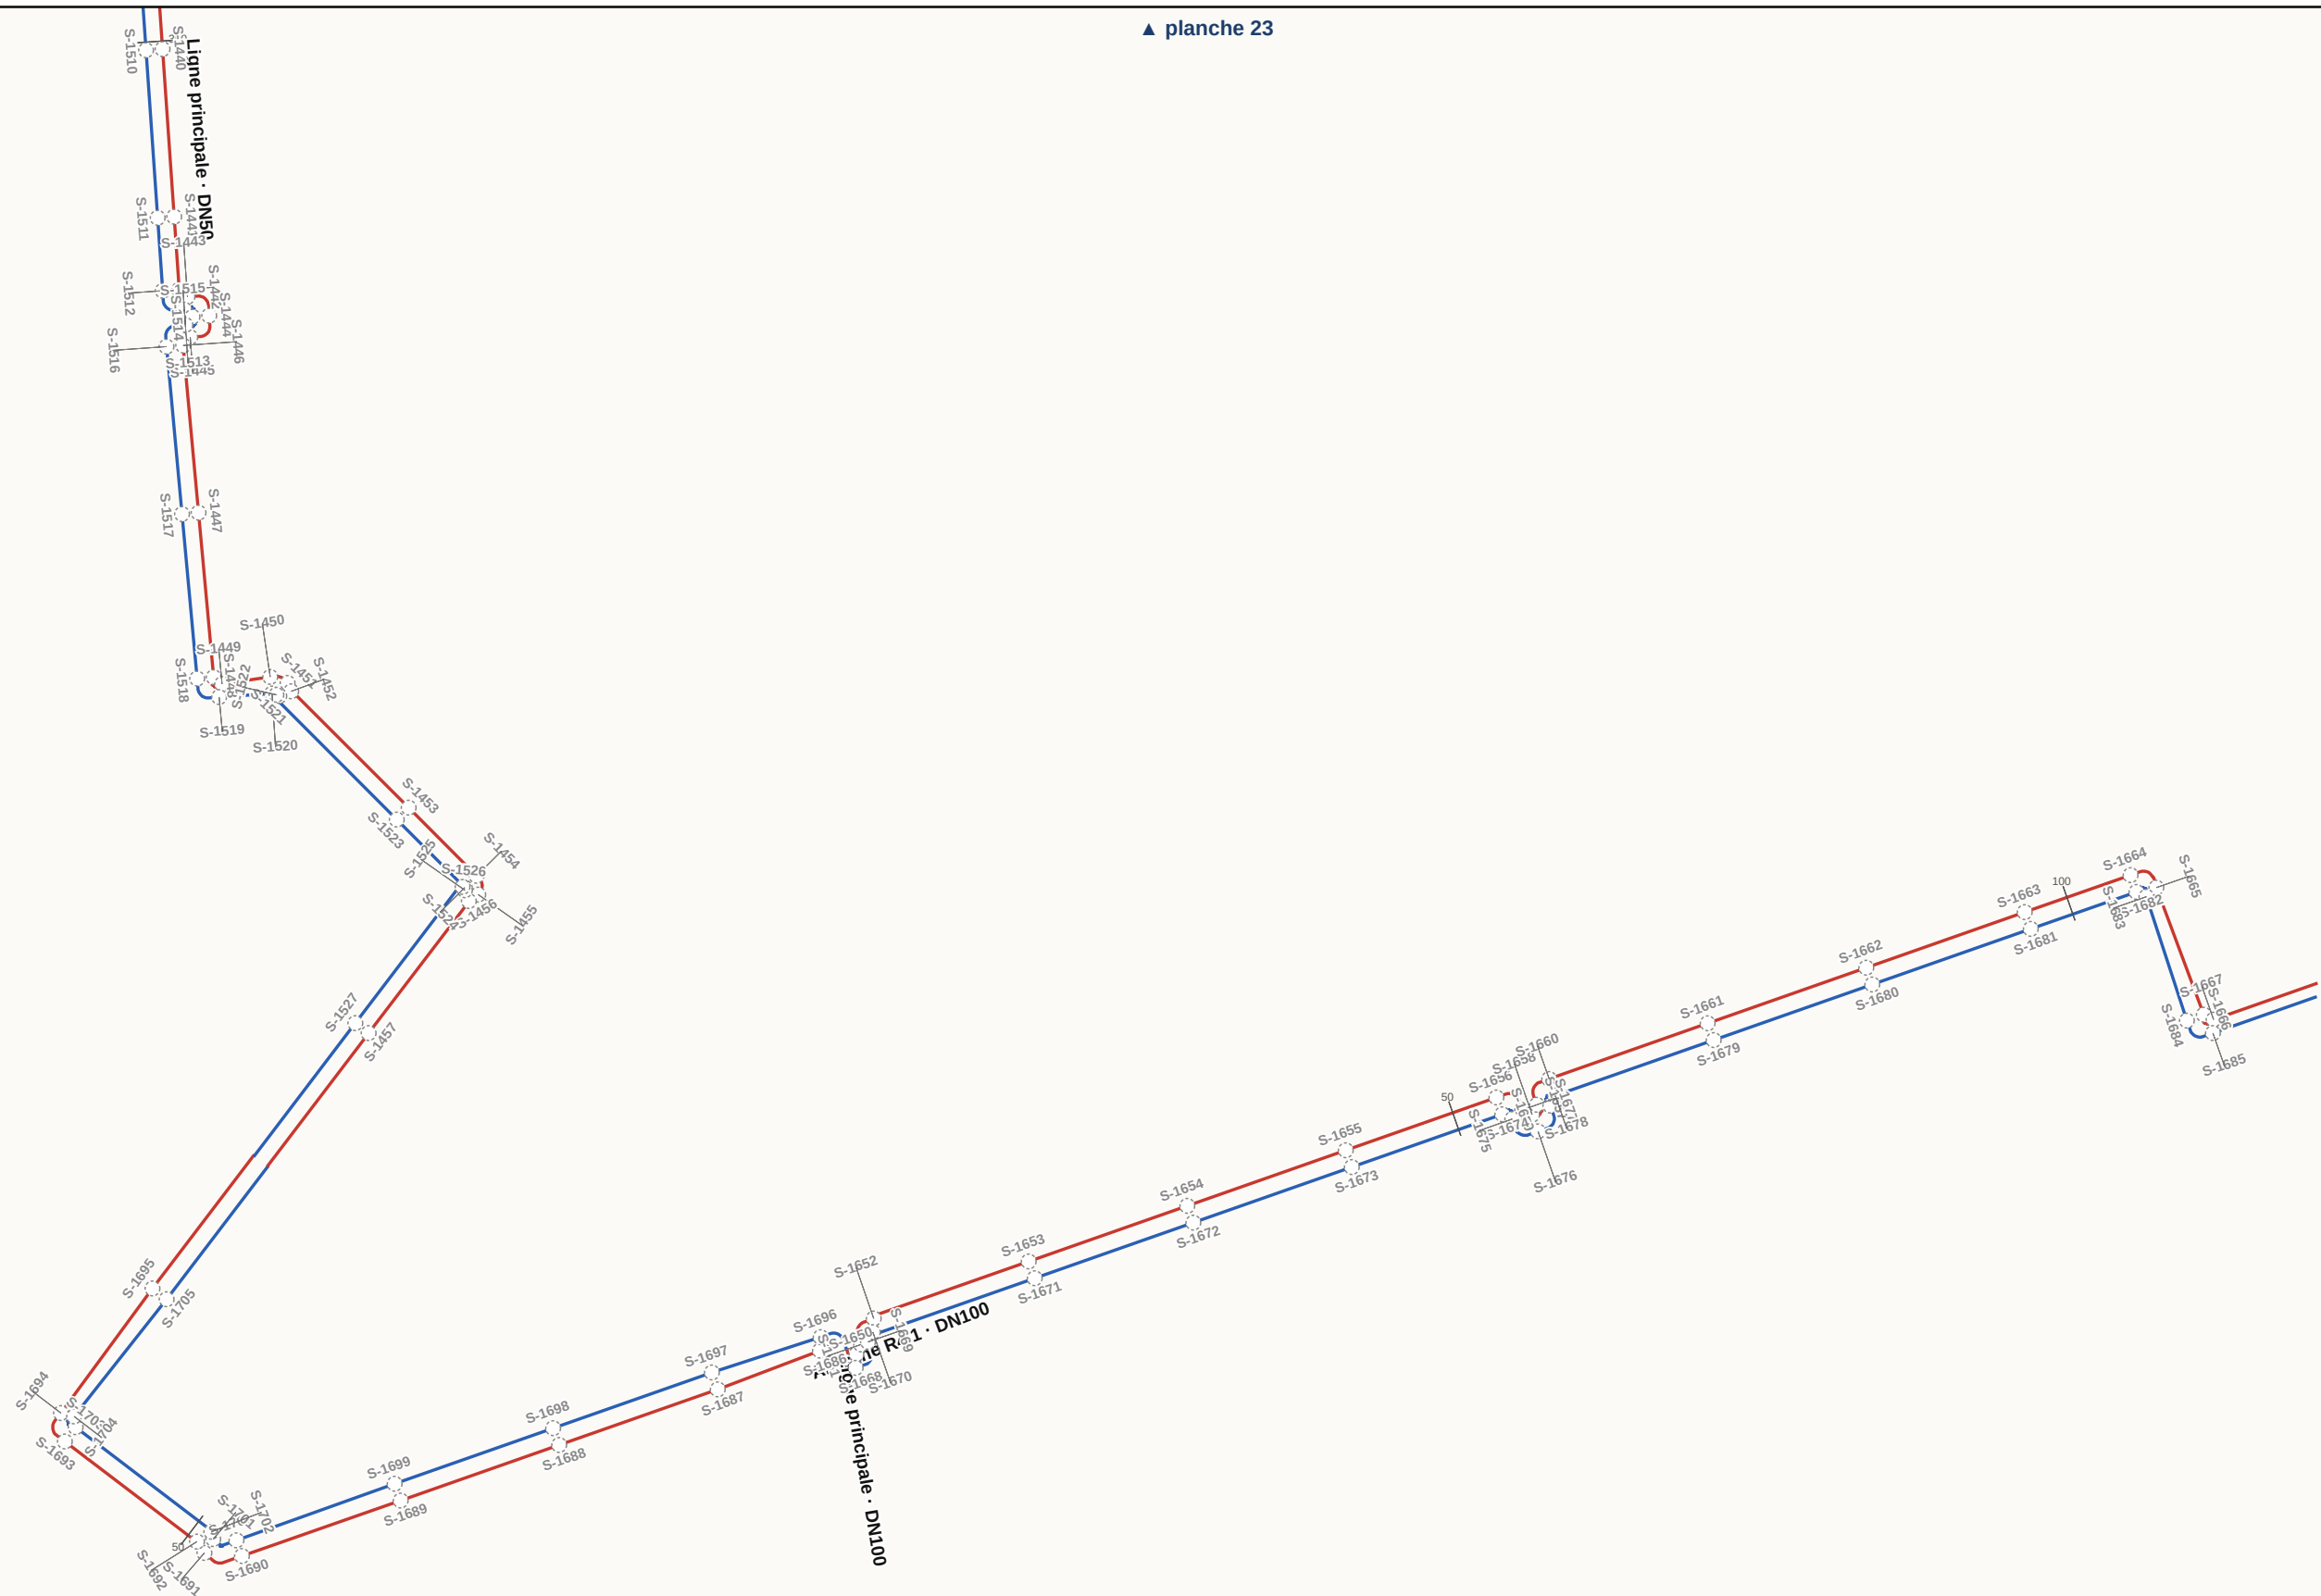

Bain-de-Bretagne — LOGSTOR (DWG calepinage)

Plan des soudures numérotées — **planche 24 / 24** · échelle 1/500 sur A3

Bain-de-Bretagne — LOGSTOR (DWG calepinage) · report du carnet de soudage et manchonnage · n° = n° de soudure (pastille = avancement)

À souder
 Soudée
 Contrôlée
 Manchonnée
 À reprendre
 aller
 retour
 vanne
 réduction
 té